

Shalung und Bewehrung FT.- Wandplatte-Achse A-W505.1

M 1:25

Bewehrung

M 1:25

Schnitt a-a

M 1:25

Einbauteilleiste (je Fertigteil)				
EBT - Nummer	Hersteller	Bezeichnung	Korrosionsschutz	Menge (Stück)
00104	Hallen	HTA-38/17-FV-150	FV	3
00803	Hallen	HTA-54/32-FV-200	FV	5
09116	Philipp	GWA-KA RD42 385mm		4
09505	Philipp	87SA20 100mm		3
09901	Philipp	Dornhülse 72DH25		2
10000	Philipp	PDS 70/250 PHILIPP Power Duo System, l=1250mm	FV	2
10005	Philipp	PDS 20/250 PHILIPP Power Duo System, l=1250mm	FV	6
10006	Philipp	PDS 20/250 PHILIPP Power Duo System, l=750mm	FV	1
10008	Philipp	PDS 20/250 PHILIPP Power Duo System, l=500mm	FV	1
10513	Robusta	HWR 080 x 200mm		3


Montageeilleiste (je Fertigteil)				
MTT - Nummer	Hersteller	Bezeichnung	Korrosionsschutz	Menge (Stück)
12501		Bewehrung Ø25, L=35cm		1
12504		Bewehrung Ø25, L=70cm		2

Lastausgleichsgehänge !!

Alle Maße der Betonstahlauszüge sind Außenmaße!

letzte Stabstahlposition 19
letzte Mattenposition

Mindestwerte für Biegerollendurchmesser D _{min} gemäß DIN EN 1992, Tab 8.1 DE			
Seitliche Beton- deckung	>10 cm und >5 cm und 5 cm und 3 cm	10x 15x 20x	D _{min}

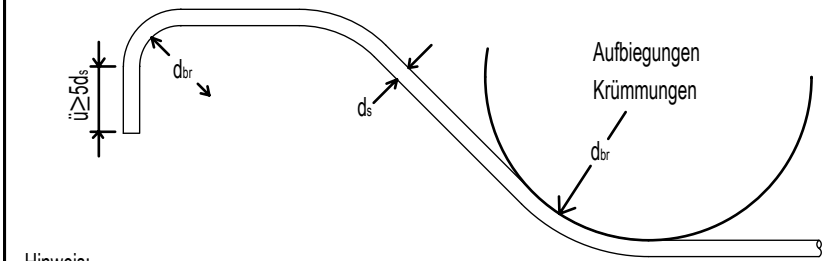

Hakenzuschlag pro Haken (15x)
Maße gelten von aussen bis aussen !

BAUTEIL:	BETONFESTIGKEIT	Expositionsklassen:	Feuchtigkeitsklasse:	BETONDECKUNG
Wand	C50/60	XC1	WO	C _{min} 15 C _{med} 10 C _s 25


Volumen	Gewicht	Anzahl	Statische Positionennummer
3.21	8.03	1	WE104

Kanten	Stückanzahl	abgelesen
1	1	1

Zugehörige Pläne:
Stahlbeton-Fertigteil Wand: BER210-HBE-ZZ-02-DR-S-WALL-8153 BER210-HBE-ZZ-02-DR-S-WALL-8155

Planfreigebe Zur Ausführung Freigegeben

General / Allgemein
OKFF = 0.000 mm = 41.80 m ü.NN/
Finished floor level = 0.000 mm = 41.80 m ü.NN

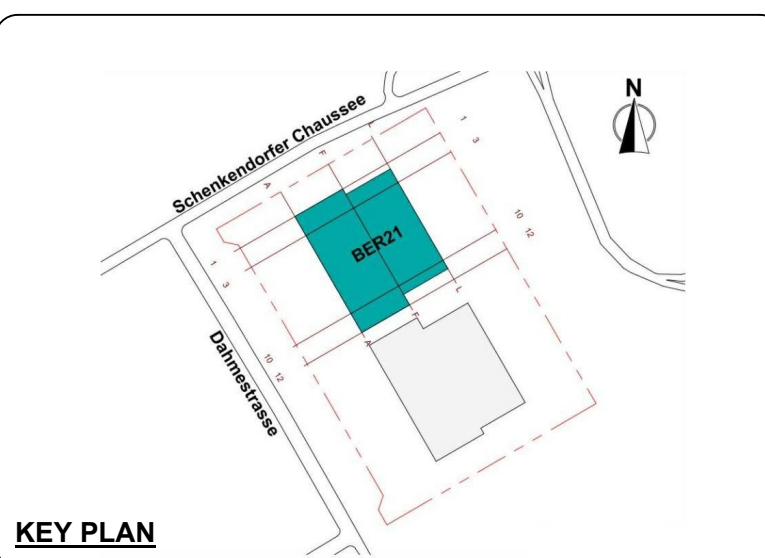

Rev	Date	Details	By	App
C02	17.03.2022	Update EBT 09505		
C01	18.02.2022	Issued for construction		
P01	24.01.2022	Issued for construction review		

Drawing Status:
Issued for Construction

Main Contractor:
MERCURY
Mercury House, Sandyford Ind. Estate, Dublin 18, Ireland
E: mail@mercuryeng.com | T: +353 1 2163000 | www.mercuryeng.com

Neue Mainzer Str. 75
60311, Frankfurt am Main
Deutschland
HRB. 111436
T: +49 171 623 25 84
E: info@de.rdhv.com
www.royalhaskoningdhv.com

Technisches Büro
Heidelberger Betonelemente
GmbH & Co. KG
Am Zeisig 9
09322 Penig / OT Wernsdorf
Tel.: 037381/857-0
Fax: 037381/857-30

FACHPLANER/PLANERSTELLER
gbc
gbc engineers GmbH
Am Spreebord 5d
10589 Berlin
Tel.: +49 (0) 30 339 38 740
Fax: +49 (0) 30 339 38 741
eMail: info@gbc-engineers.de
www.gbc-engineers.de


Client:
Vantage
Project:
BER-21

Drawing Title:
Shalung und Bewehrung FT.- Wandplatte-Achse A-W505.1
Formwork and reinforcement Pr.- Wall panel-Axis A-W505.1

Drawn By: T.Ng	Designed By: H.T	Checked By: D.M
Project No. DE1.0049.01	Scale: 1:25 1:200	Date: 24.01.2022
Drawing No. BER210-HBE-ZZ-02-DR-S-WALL-8154	Revision: C02	Status: A1


Ansicht

M 1:25

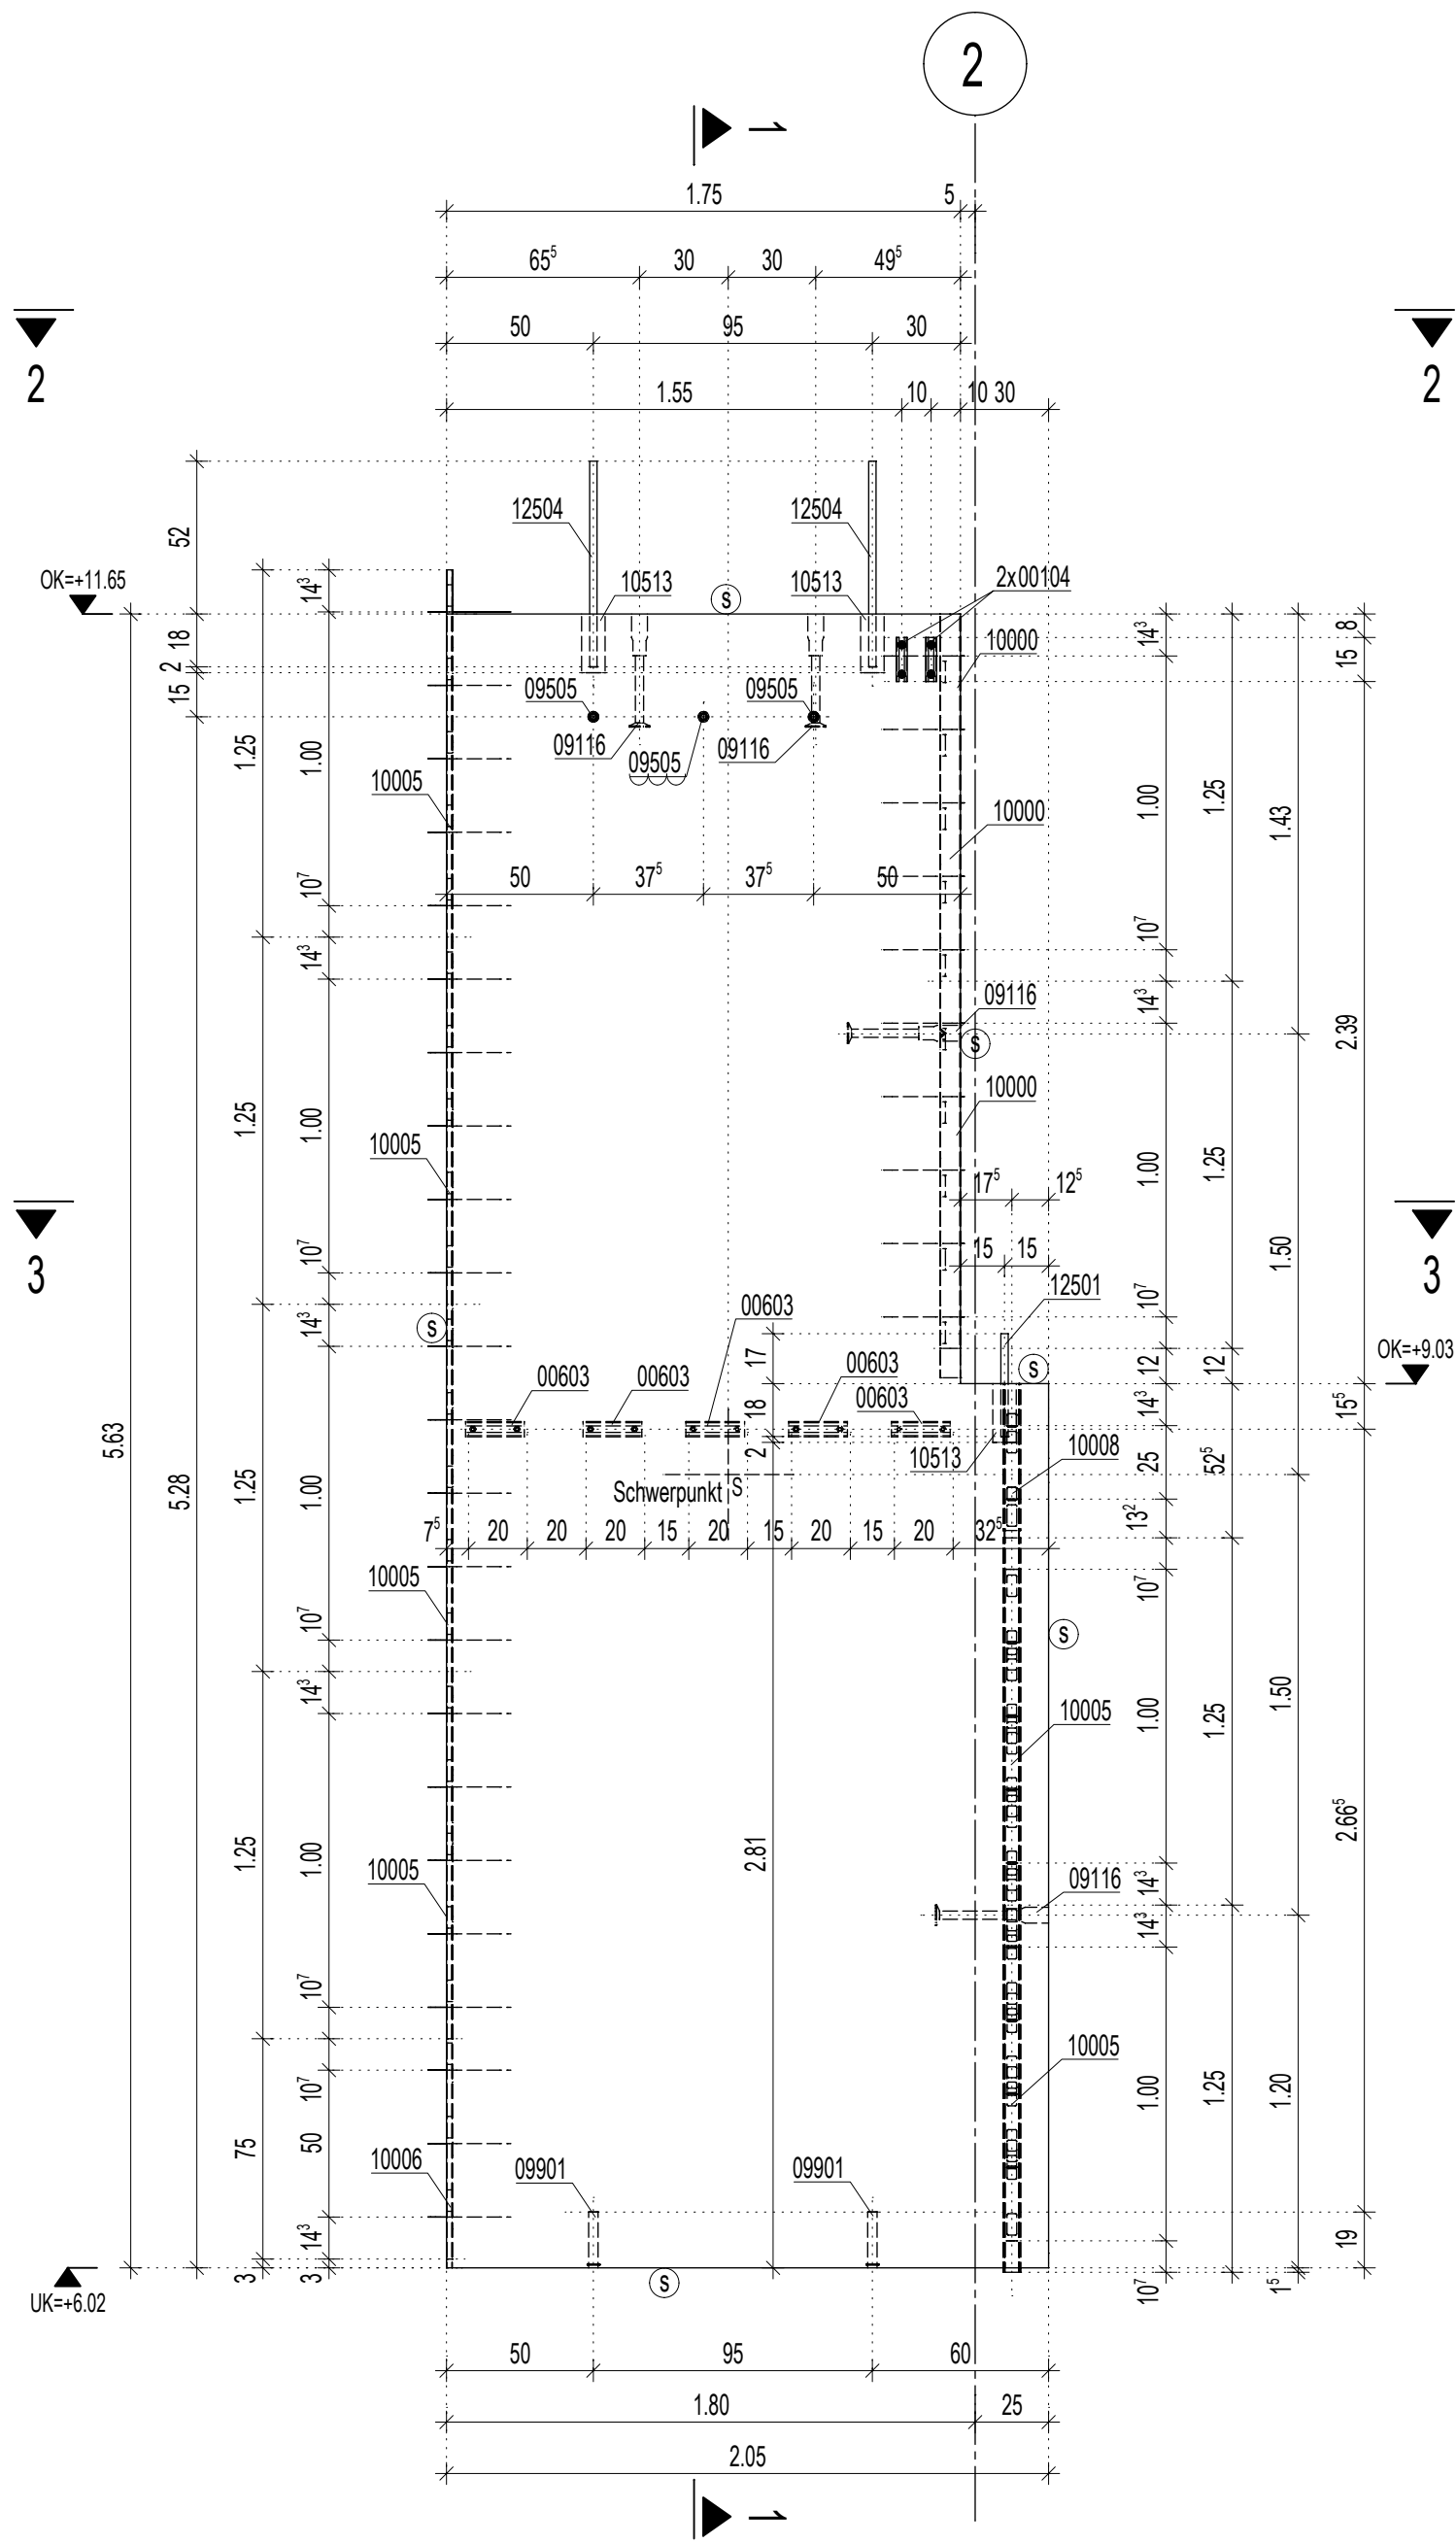

Schnitt 1-1

M 1:25

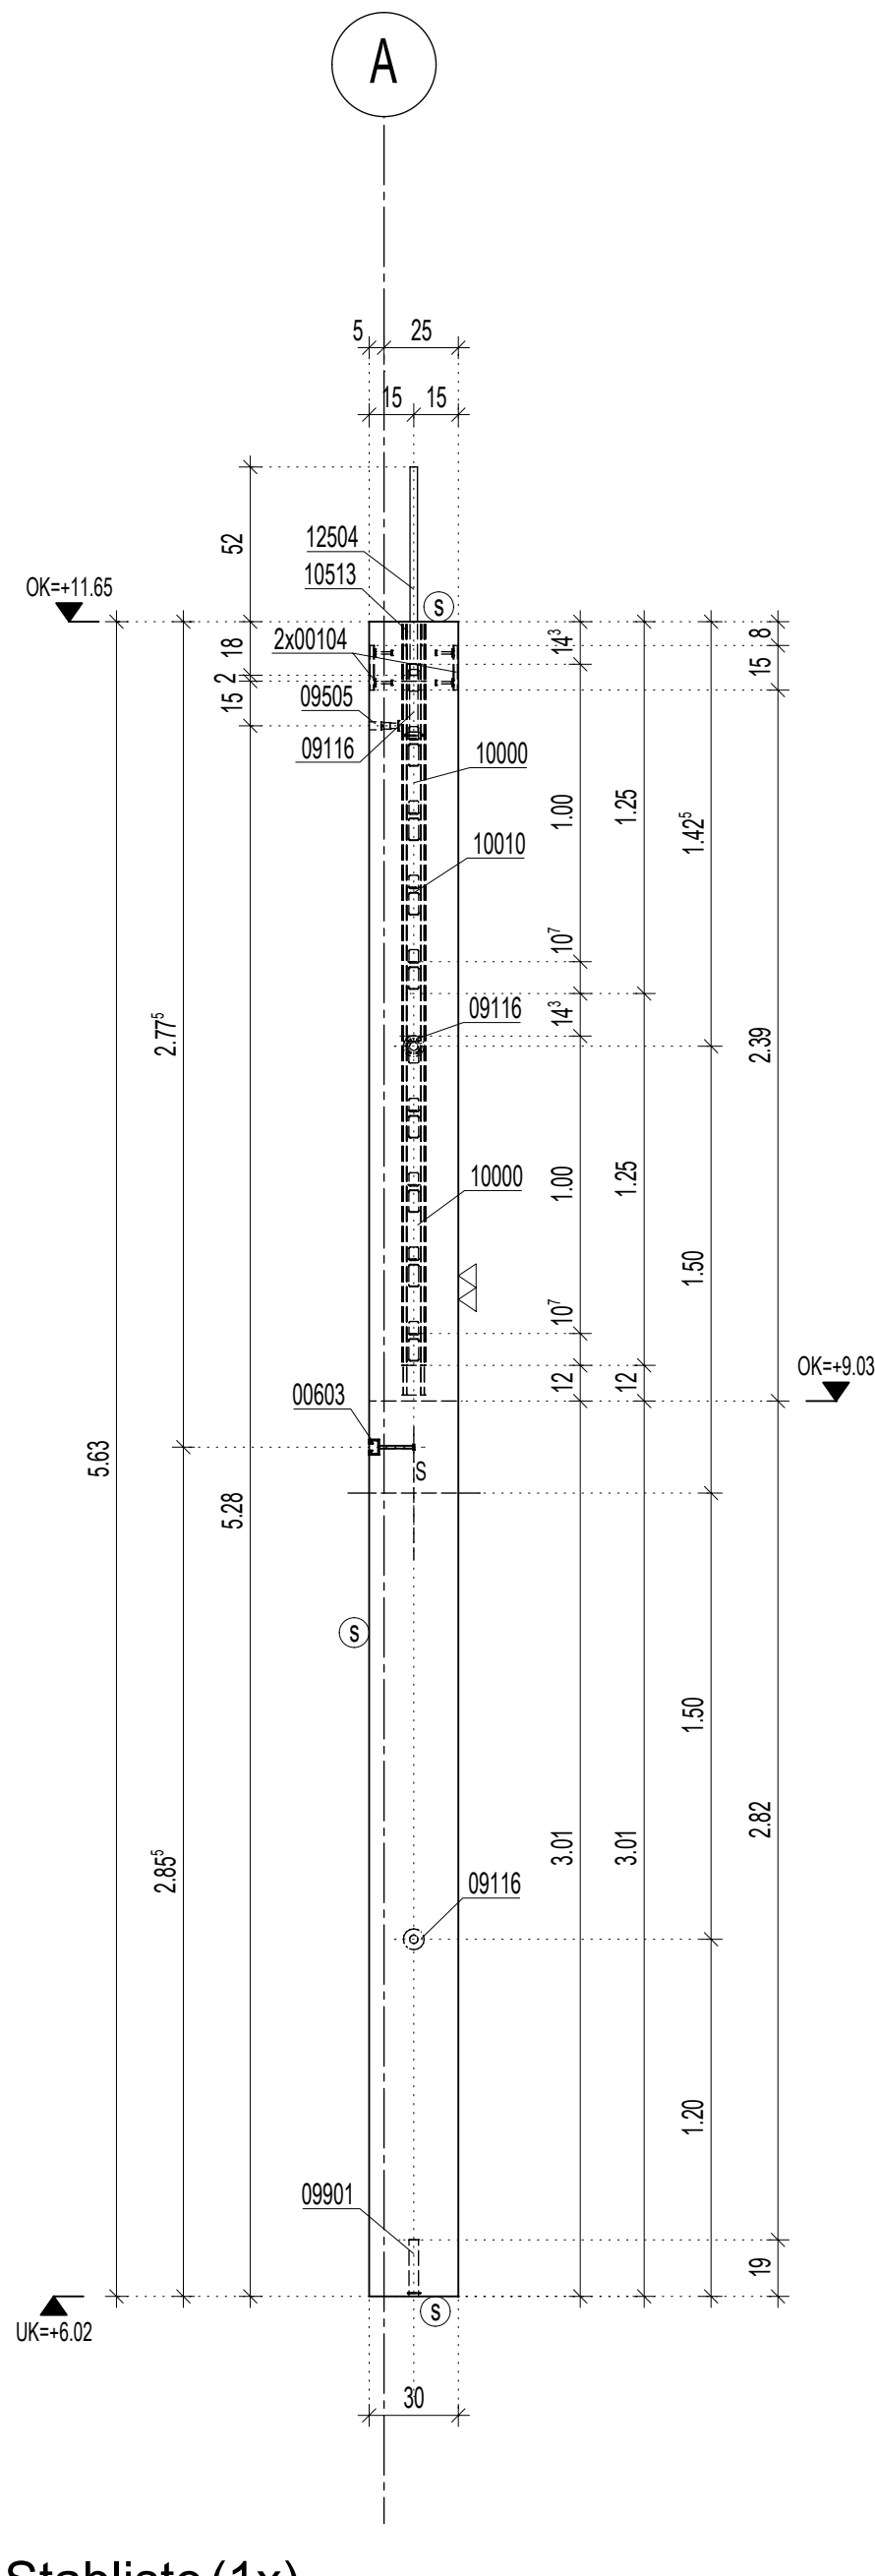


Stabliste (1x)

Pos.	Stck	ø [mm]	Einzel Länge [m]	Gesamt Länge [m]	Masse [kg]
1	36	10	1.65	59.40	36.65
2	38	10	1.95	74.10	45.72
3	4	12	2.90	11.60	10.30
4	74	10	0.92	68.08	42.01
5	15	12	1.05	15.75	13.99
6	4	12	1.90	7.60	6.75
7	8	12	1.10	8.80	7.81
8	2	16	3.15	6.30	9.95
9	4	12	1.25	5.00	4.44
10	2	16	2.85	5.70	9.01
11	12	10	0.80	9.60	5.92
12	22	12	5.55	122.10	108.42
13	2	16	5.45	10.90	17.22
14	2	12	3.15	6.30	5.59
15	2	14	2.55	5.10	6.17
16	2	20	1.55	3.10	7.66
17	42	8	0.43	18.06	7.13
18	2	16	0.90	1.80	2.84
19	11	12	1.45	15.95	14.16
100	3	8	0.65	1.95	0.77
101	16	8	1.22	19.52	7.71
102	4	16	1.14	4.56	7.20
103	4	16	1.00	4.00	6.32
104	2	20	1.73	3.46	8.55

Gesamtmasse [kg]: 362.29


Schnitt b-b

M 1:25

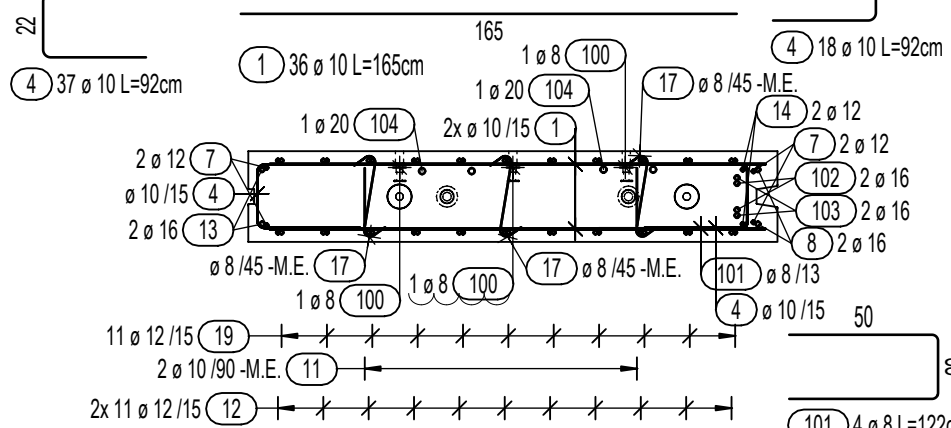


Schnitt c-c

M 1:25

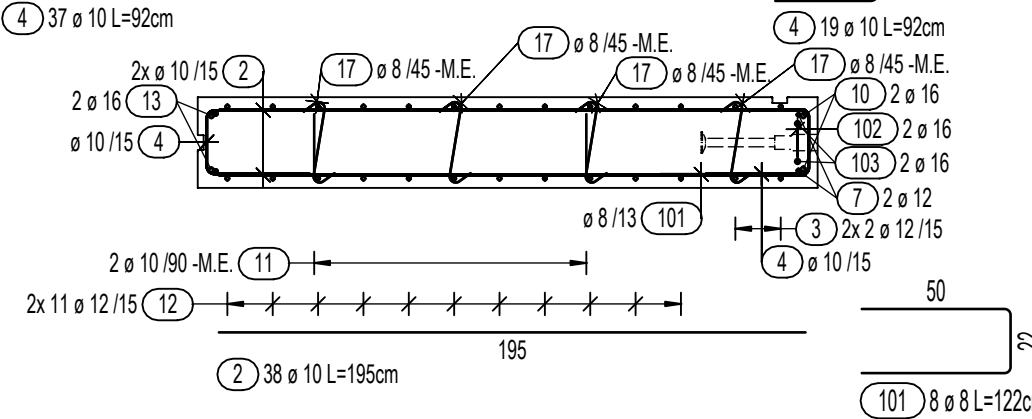


Wandansicht Achse A

M 1:200

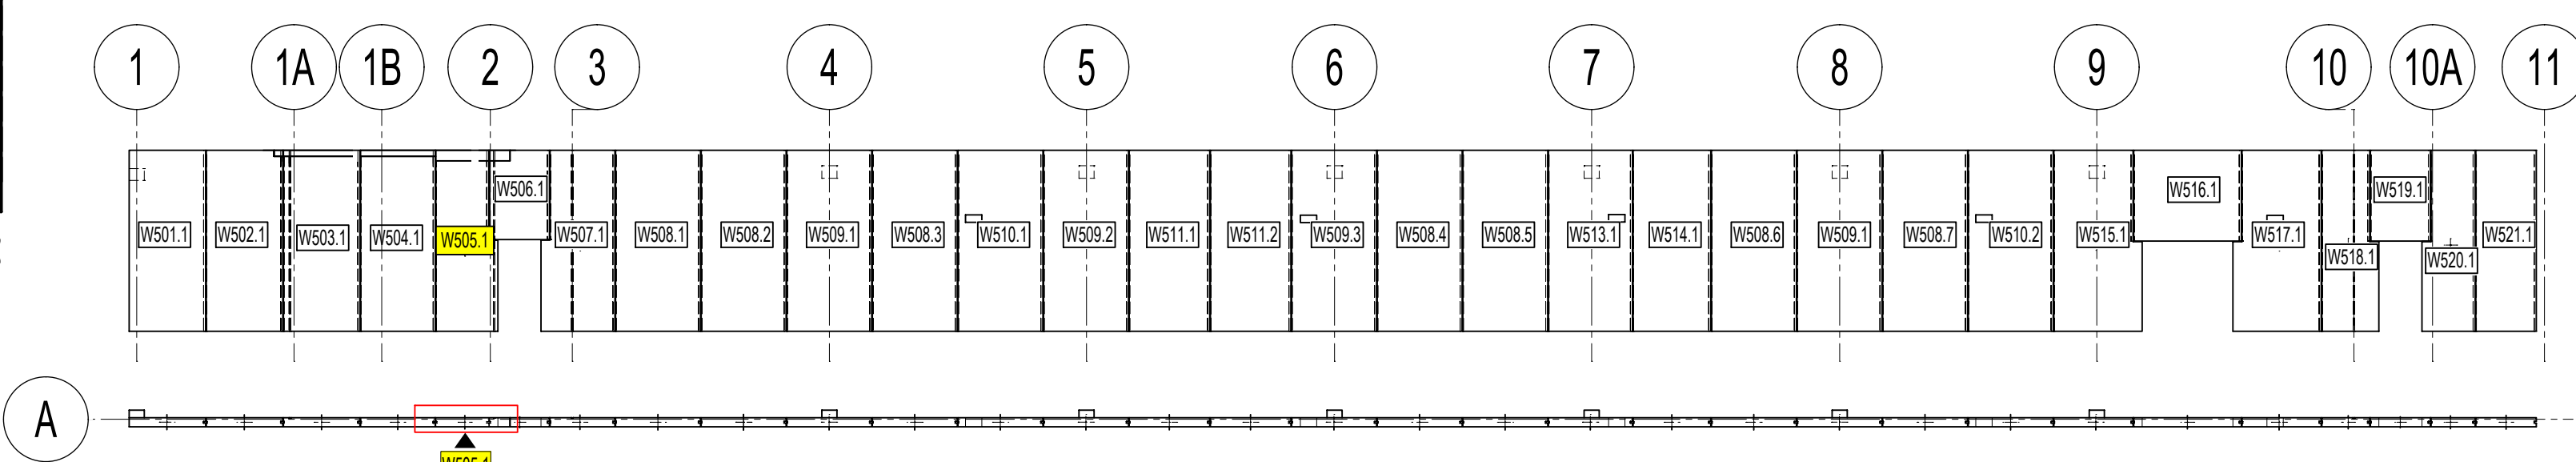

Draufsicht 2-2

M 1:25

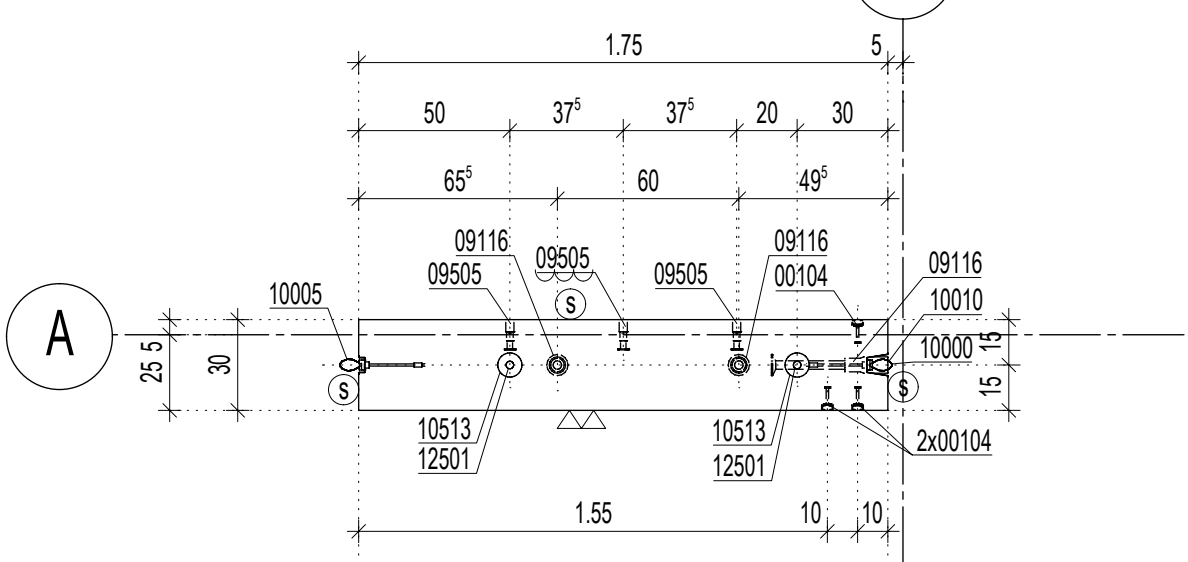

Schnitt 3-3

M 1:25

