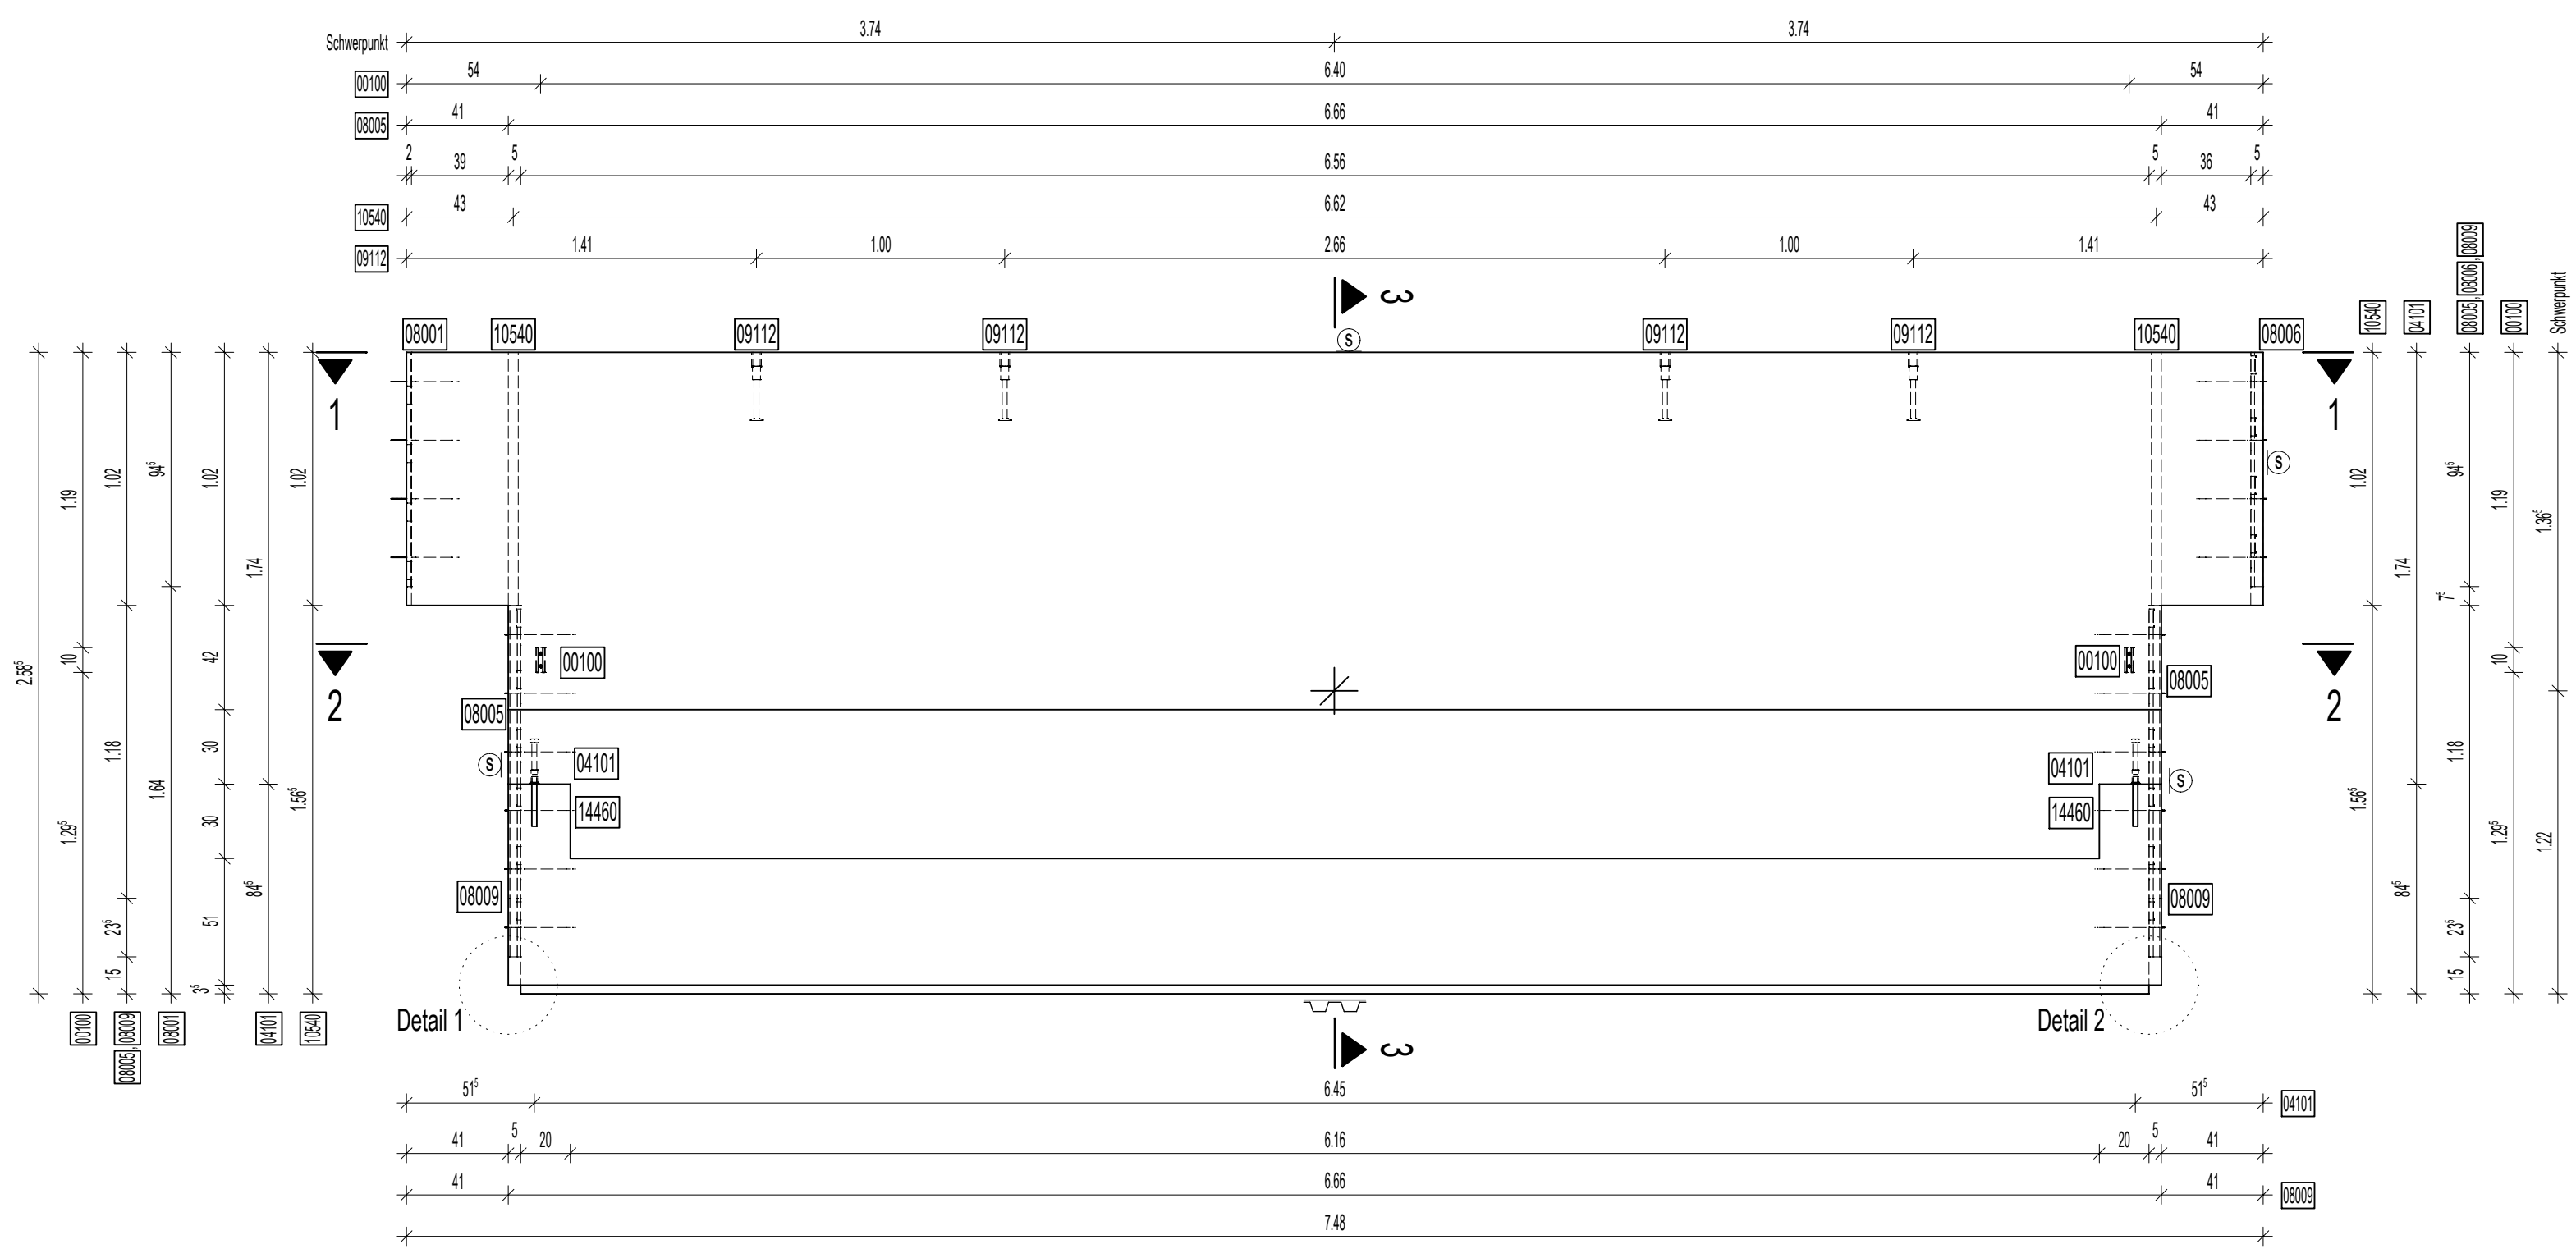
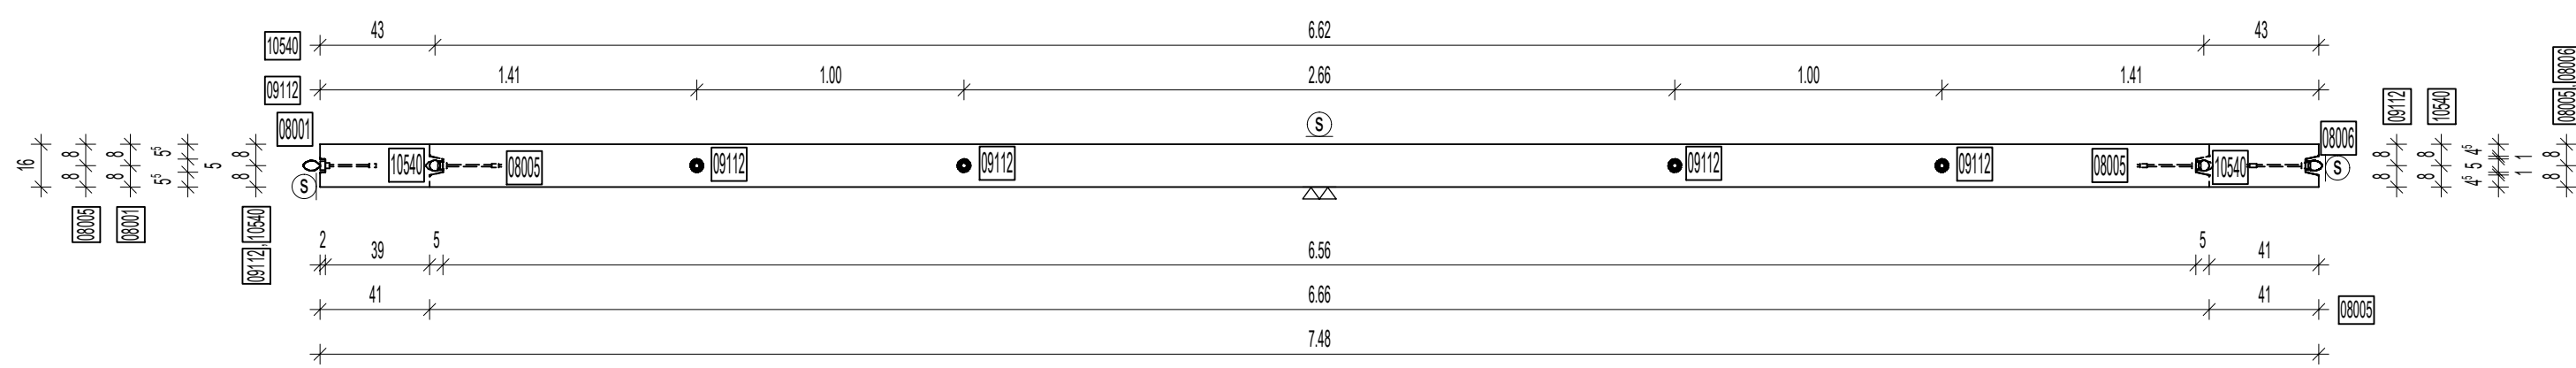
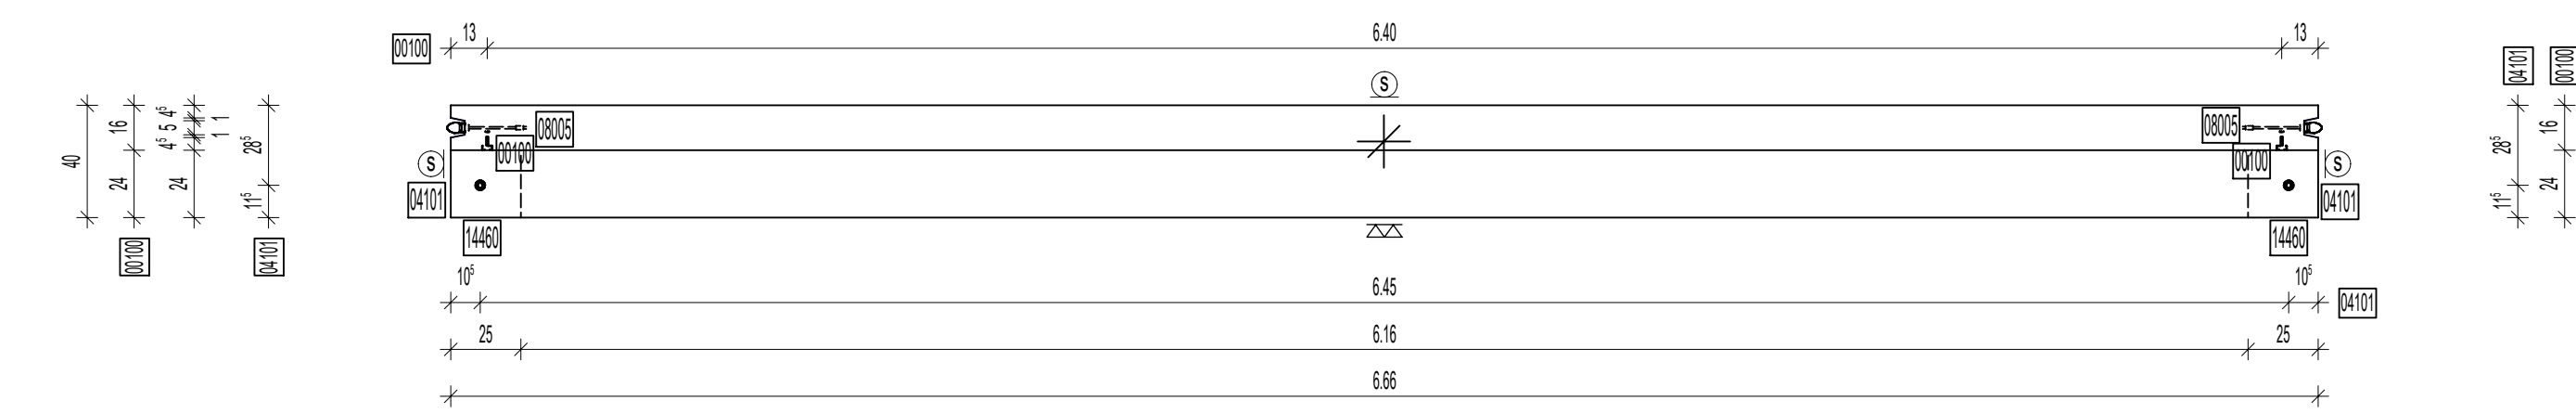
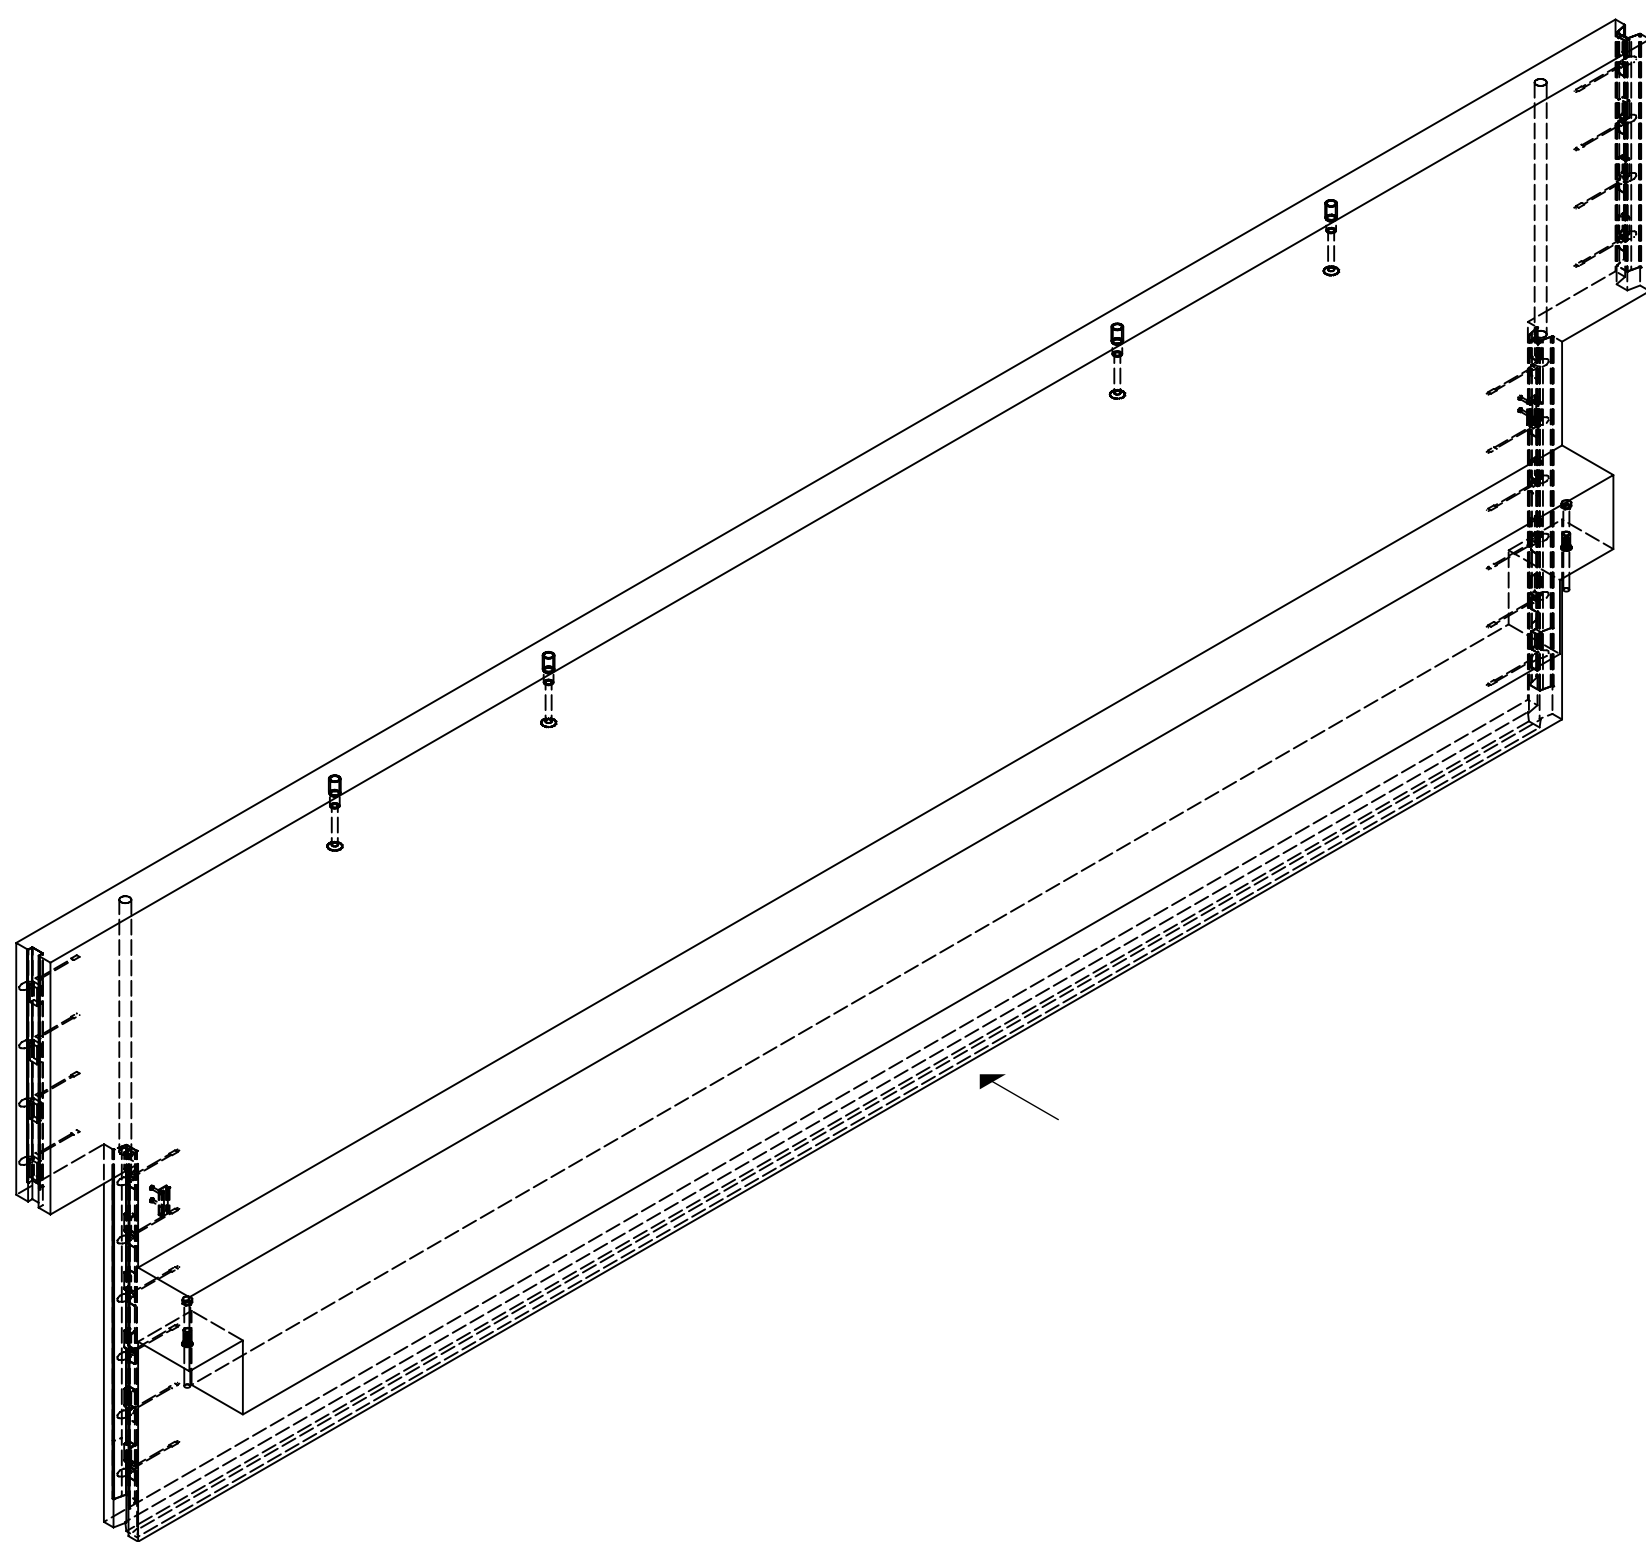
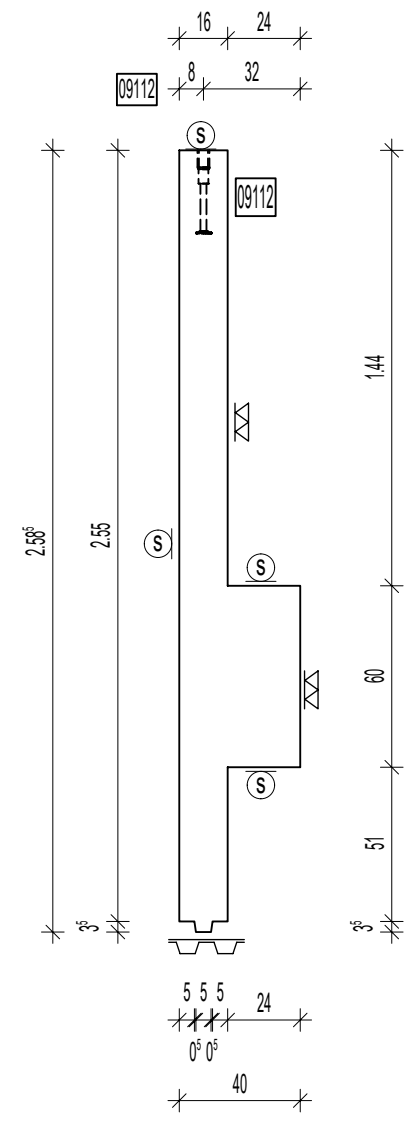
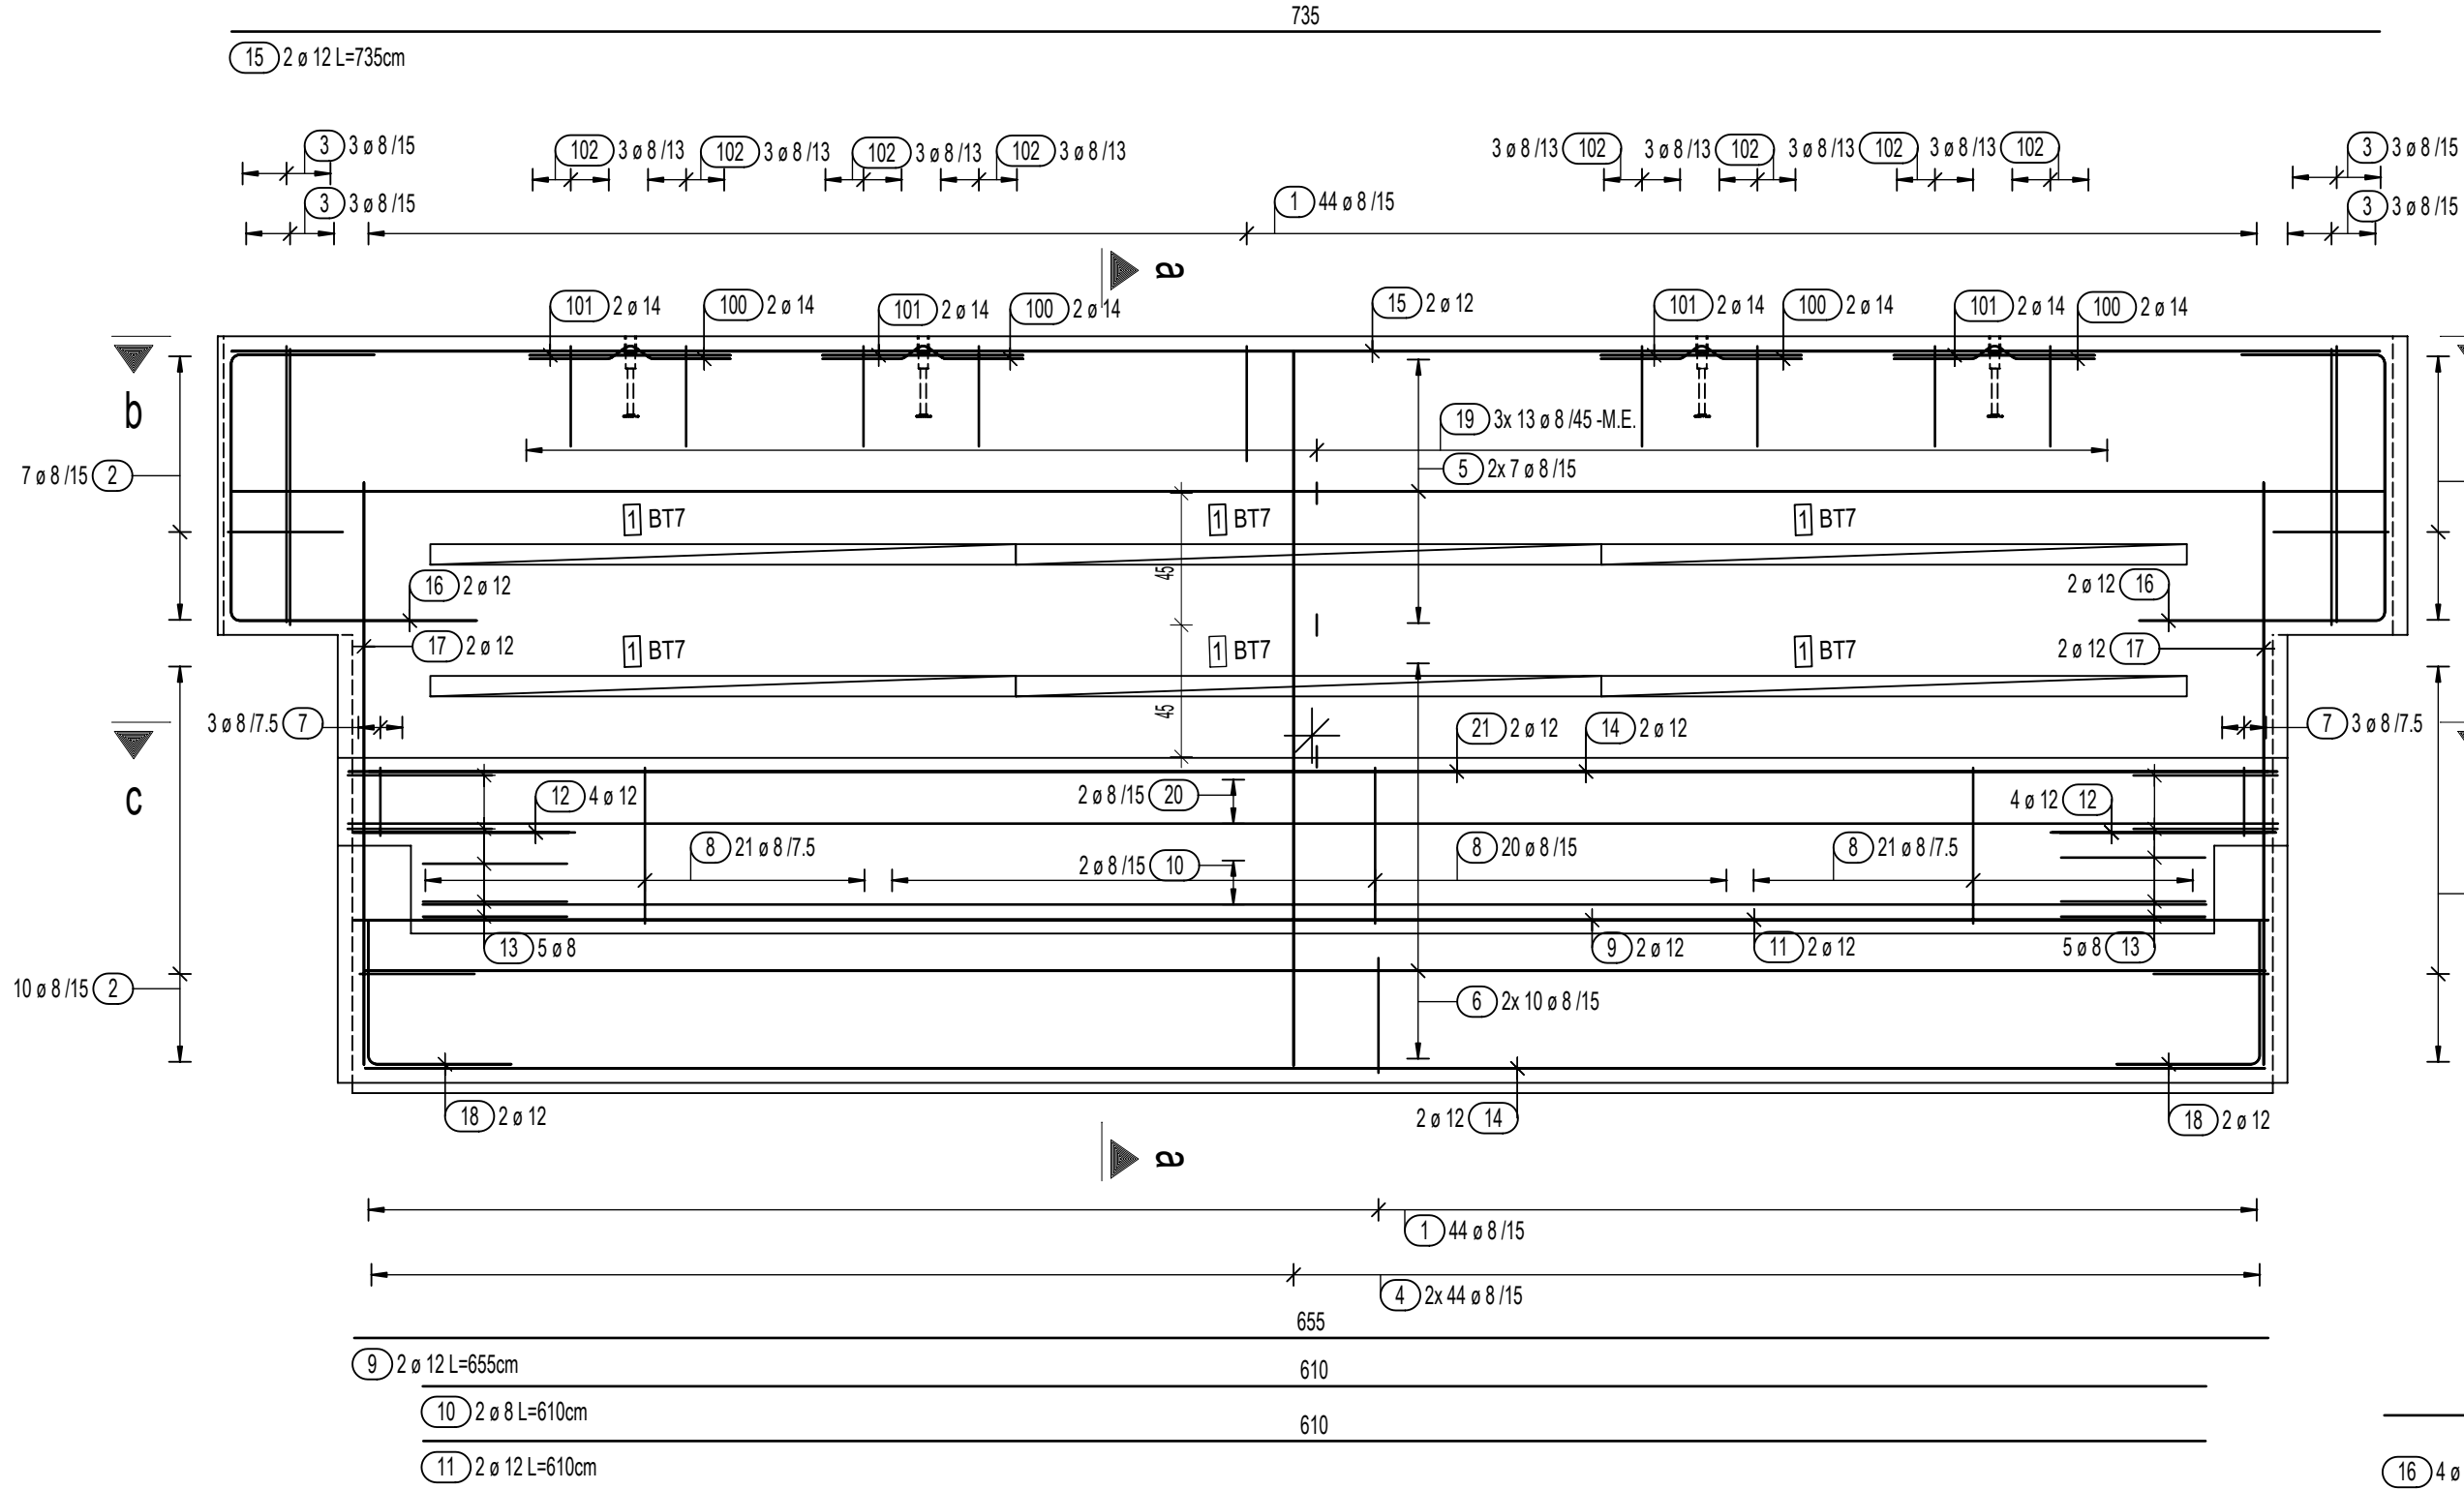
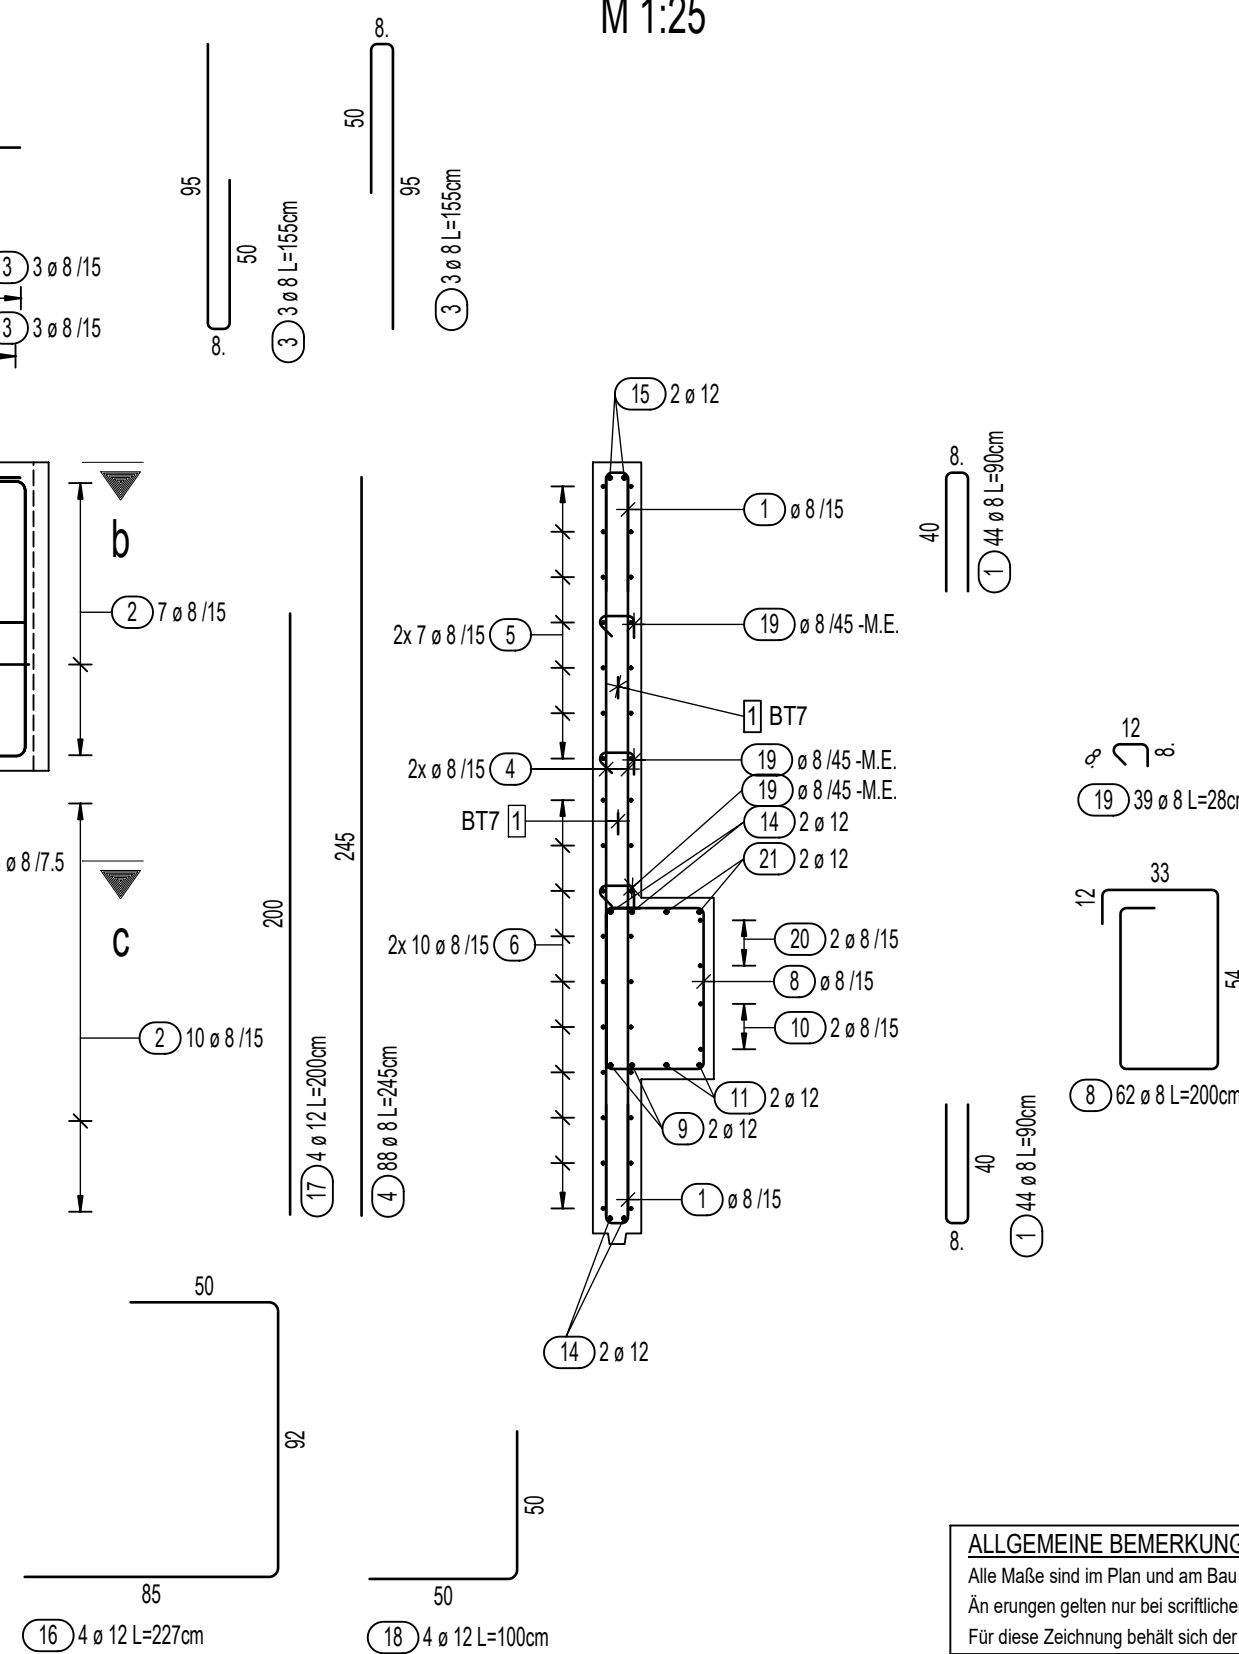


Ansicht
M 1:25Draufsicht 1-1
M 1:25Schnitt 2-2
M 1:253D Perspektive
M 1:25Schnitt 3-3
M 1:25Bewehrung
M 1:25Schnitt a-a
M 1:25

ALLGEMEINE BEMERKUNGEN:
Alle Maße sind im Plan und am Bau zu überprüfen! Abweichende oder falsche Maße sind dem Planverfasser und/oder dem Bauleiter schriftlich zu melden!
Anfragen gelten nur bei schriftlicher Bestätigung des Planverfassers und der Doppelzeichnung als anerkannt.
Für diese Zeichnung behält sich der Planverfasser alle Rechte vor. Vervielfältigungen dürfen nur mit ausdrücklicher Genehmigung des Planverfassers erfolgen.

ABKÜRZUNGEN UND SYMBOLE

= Änderung = in Klärung

BAUSTOFFE (SOWEIT NICHT ANDERS ANGEBOGEN)

Kanten soweit nichts anderes angegeben ist, sind zu fassen
Faserstärke: $\geq 1.5 \text{ cm}$

Symbol	Bezeichnung
	Betonklasse (B8)
	Stabtypen (SB)
	Fluglänge
	Stützungslänge

MINDESTWERTE DER BIEGERADIIEN DBR (EC2, TABELLE 8.1 + 8.2)

Haken, Winkelhaken, Schlaufen	Stabkrümmungen
Stabdurchmesser	Haken, Schlaufen, Bügel
ds > 20 mm	7 ds
ds > 20 mm	4 ds
Betondeckung rechteckig zur Krümmungsebene	Aufbiegen und andere Krümmungen von Stäben (Rahmenecken)
> 100 mm oder > 7ds	10 ds
> 50 mm und > 3ds	15 ds
≤ 50 mm oder ≤ 3 ds	20 ds

Die Gesamtlängen der Auszüge beziehen sich auf Außenmaße!

letzte Stabstahlposition			(21)	letzte Mattemposition			(1)
Bauteil:	Betonfestigkeit	Expositionsklassen:	Feuchtheitsklasse:	Betondeckung:			
				C _{min} in cm	C _{max} in cm	C:	
FT-Brandwand	C30/37	XC2	WO	20	10	30	
Volumen	Gewicht	Anzahl	Statische Positionsnummer				
3.774 m³	9.262 T	9	HL-07-10				

<u>ZUGEHÖRIGE PLÄNE</u>	
Übersichtsplan Wandansichten	REN-HL-KO-TK-W-UB-E00-4500
Ansichten - Brandwände Teil 2 - Achse C/5-11	REN-HL-KO-TK-W-UB-E00-4502

PLAN STATUS

ZUR AUSFÜHRUNG FREIGEgeben

INDEX	DATUM	ÄNDERUNG	GEÄNDERT
01	23.08.2023	Freigegeben durch Prüfingenieur am 23.08.2023 und Architekt am 24.07.2023	N.P.V.
00	10.07.2023	Entwurfslieferung	N.P.V.

OKRD = > 36,50 m u. N.N.	Bemessungsgrundwasserstand < -2,00 m GOK	OKRFB = > 36,50 m u. N.N.
--------------------------	--	---------------------------

Plannummer Tragwerksplanung:
Projekt-Gebäude-Fachbereich-Gewerk-Phase-Planart-Ebene-Plannummer-Index-Status
REN-HL-KO-TK-W-FT-E01-1528-01-F

Beispiel:
Projekt: **Produktionswerk Renggli DE**

Bauherr: **Renggli Deutschland GmbH**
Am Bahnhof Westend 9-11
14059 Berlin

Technisches Büro
Heidelberger Betonelemente GmbH & Co. KG
Am Zewig 9
09322 Pöngitz / OT Wernsdorf
Tel.: 0373819857-0 | Fax: 0373819857-30

Fachplaner:
gbc engineers GmbH
Am Spreebord 9d
10589 Berlin
Tel.: +49 (0) 30 339 38 740 | Fax: +49 (0) 30 339 38 741 | eMail: info@gbc-engineers.de

Zeichnung: **Fertigteileplan Brandwand W-528-01**




Projekt-Nr.:	30-0-033	Planungsphase:	Ausführungsplanung
Blattgröße:	841x1189mm	gezeichnet:	N.P.V.
Maßstab:	1:25 1:5	geprüft:	D.M.
		Datum:	10.07.2023
		Datum:	10.07.2023

Einbauteilleiste (je Fertigteil)

EBT - Nummer	Hersteller	Bezeichnung	Korrosionsschutz	Menge (Stück)
01003	Hallen	HTA-38/17-FV-100	Feuerverzinkt	2
04101	Hallen	DEMU 1989 PV M2x180	Feuerverzinkt	2
06001	Pfeiler	VS-IS-20, L=944 mm		1
06005	Pfeiler	VS-IS-50, L=1189 mm		2
06006	Pfeiler	VS-IS-50, L=944 mm		1
06009	Pfeiler	VS-IS-50, L=208 mm		2
09112	Philipp	Kompaktanker GWA-R030 275mm		4
10540	Robusta	HWR Ø40 x 1020mm		2

Lastausgleichshänge !!**Montageteilleiste (je Fertigteil)**

MTT - Nummer	Hersteller	Bezeichnung	Korrosionsschutz	Menge (Stück)
14460		Gewindestorn M20 x 200 mm, Güte 8.8		2

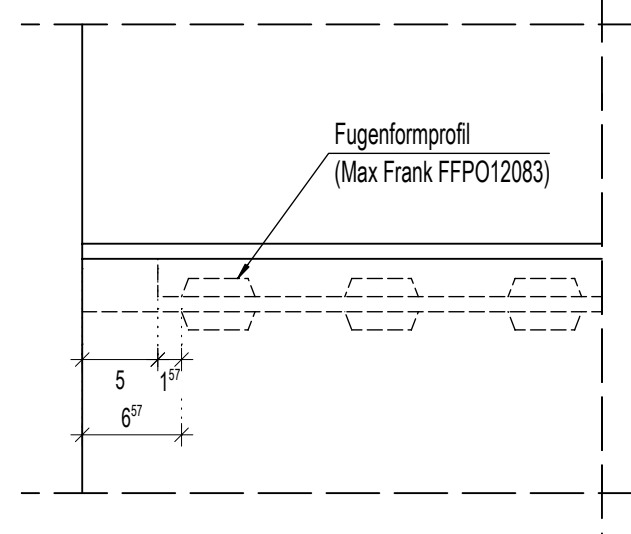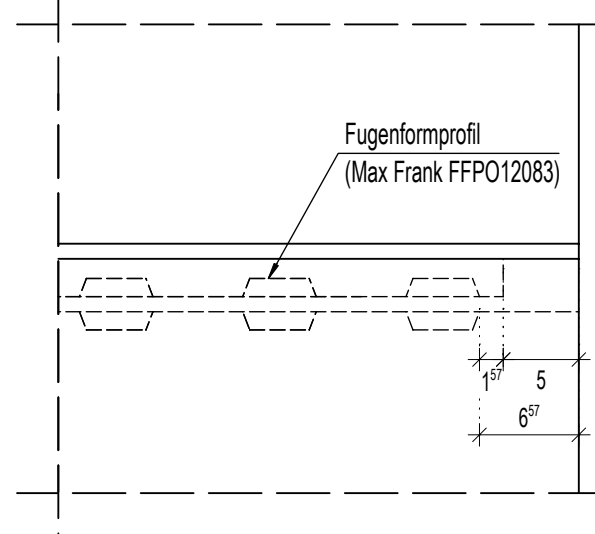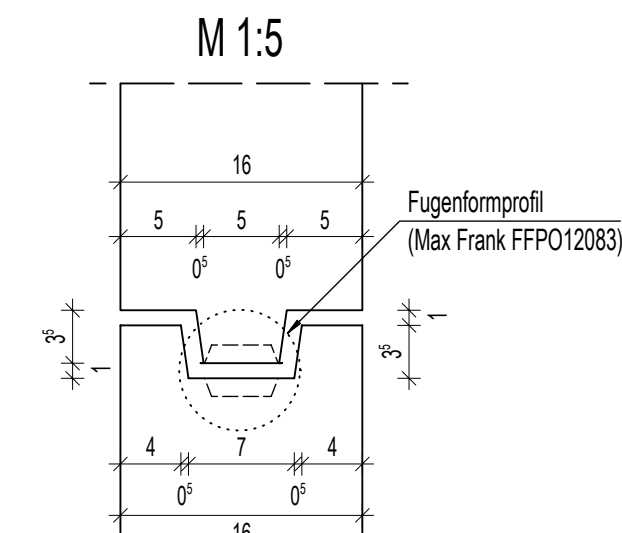Ansicht Stoßfuge - Detail 1
M 1:5Ansicht Stoßfuge - Detail 2
M 1:5Detail Stoßfuge
M 1:5**Mattenstahlstele (1x)**

Pos.	Stück	Mattenbez.	Länge [m]	Breite [m]	Gewicht [kg]
1	6	BT7	2.000	0.070	4.79
Gesamtgewicht [kg]: 4.79					

Matten- Schneideskizze

No.pcs	Name	Gross [kg]	Net weight [kg]
6	BT7	4.79	4.79
6	Total	4.79	4.79

Stablstele (1x)

Pos.	Stück	Ø [mm]	Einzel Länge [m]	Gesamt Länge [m]	Masse [kg]
1	88	8	0.88	77.44	30.59
2	34	8	0.90	30.60	12.09
3	12	8	1.53	18.36	7.25
4	88	8	2.45	215.60	85.16
5	14	8	7.35	102.90	40.65
6	20	8	6.50	130.00	51.35
7	6	8	1.38	8.28	3.27
8	62	8	2.00	124.00	48.98
9	2	12	6.55	13.10	11.63
10	2	8	6.10	12.20	4.82
11	2	12	6.10	12.20	10.63
12	8	12	0.75	6.00	5.33
13	10	8	1.23	12.30	4.86
14	4	12	6.50	26.00	23.09
15	2	12	7.35	14.70	13.05
16	4	12	2.27	9.08	8.06
17	4	12	2.00	8.00	7.10
18	4	12	1.00	4.00	3.55
19	39	8	0.28	10.92	4.31
20	2	8	6.50	13.20	5.21
21	2	12	6.50	13.20	11.72
100	8	14	0.90	6.40	7.74
101	8	14	0.70	5.60	6.78
102	24	8	0.78	18.72	7.39
Gesamtmasse [kg]:					414.81