



W-577-01

Ansicht
M 1:25

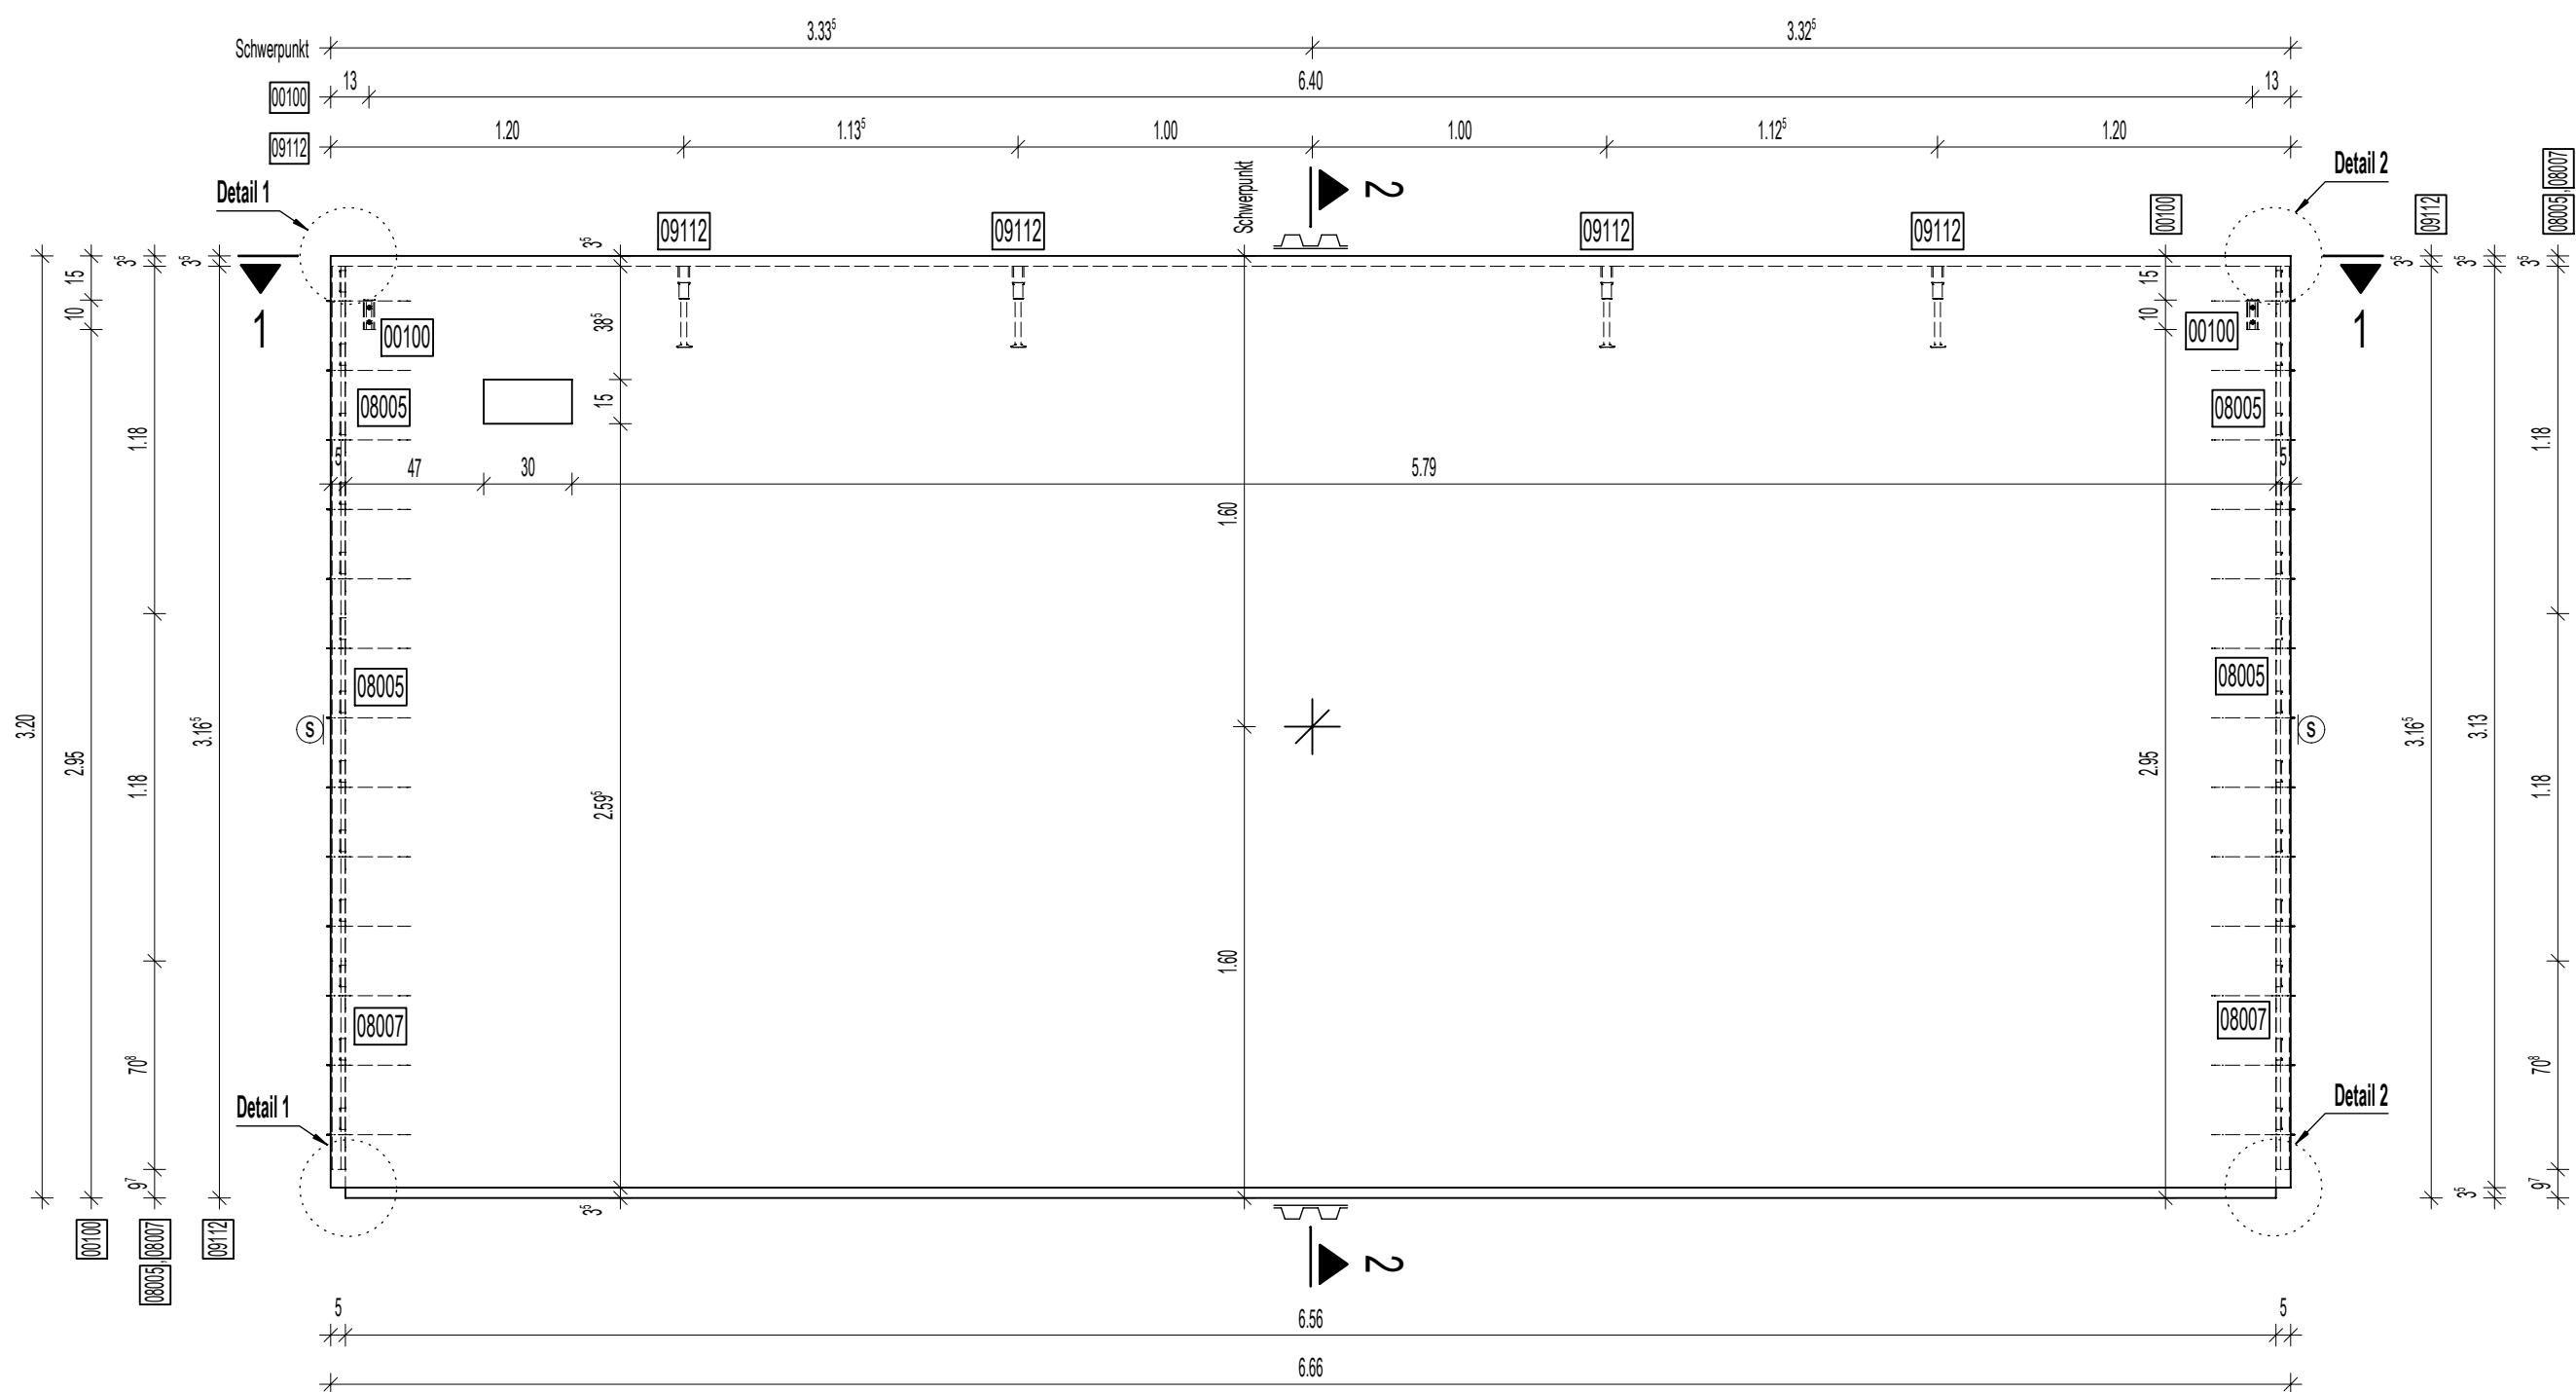

Schnitt 2-2
M 1:25

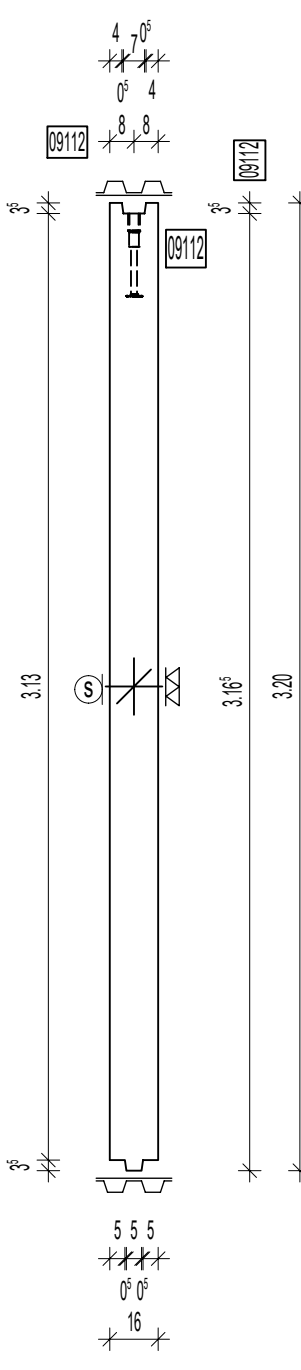

Einbauteilliste (je Fertigteil)

EBT - Nummer	Hersteller	Bezeichnung	Korrosionsschutz	Menge (Stück)
00100	Hallen	HTA-3817-FV-100	Feuerverzinkt	2
08005	Pfeiler	VS-ISI-50, L=1180 mm		4
08007	Pfeiler	VS-ISI-50, L=708 mm		2
09112	Philipp	Kompaktanker GWA-RD30 275mm		4


Lastausgleichsgehänge !!

Mattenstahlliste (1x)

Pos.	Stück	Mattenbez.	Länge [m]	Breite [m]	Gewicht [kg]
1	2	Q257A	1.280	2.300	24.23
2	4	Q257A	1.560	2.300	59.07
3	2	Q257A	6.000	2.300	113.60
4	6	BT7	2.000	0.070	4.79
5	2	Q257A	1.560	1.900	24.40

Gesamtgewicht [kg]: 226.09

Detail Stoßfuge
M 1:5

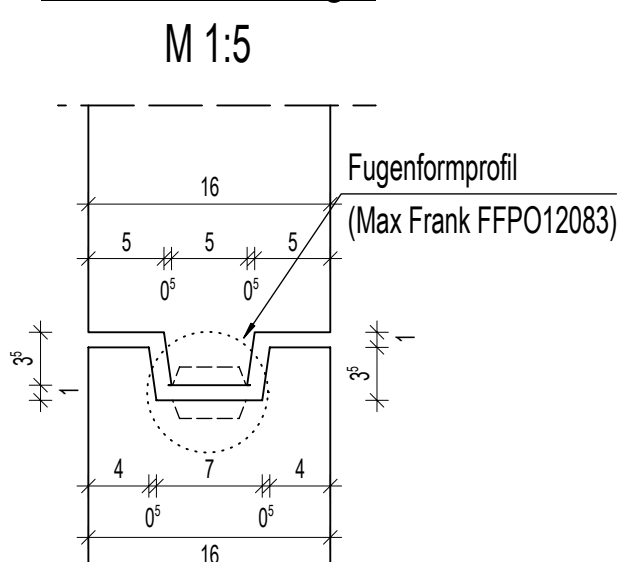

Stabliste (1x)


Pos.	Stck	ø [mm]	Einzel Länge [m]	Gesamt Länge [m]	Masse [kg]
1	70	8	0.28	19.60	7.74
2	4	12	6.45	25.80	22.91
3	4	12	2.95	11.80	10.48
4	8	12	1.20	9.60	8.52
5	4	12	1.20	4.80	4.26
6	14	8	0.90	12.60	4.98
7	2	8	1.02	2.04	0.81
8	4	12	1.25	5.00	4.44
9	24	8	0.70	16.80	6.64
10	2	8	0.88	1.76	0.70
100	24	8	0.78	18.72	7.39
101	8	14	0.80	6.40	7.74
102	8	16	0.70	5.60	8.85

Gesamtmasse [kg]: 95.46


Matten- Schneideskizze

No.pcs	Name	Gross [kg]	Net weight
4	Q257A	227.20	221.31
6	BT7	4.79	4.79
10	Total	231.99	226.09


Ansicht Stoßfuge - Detail 1
M 1:5

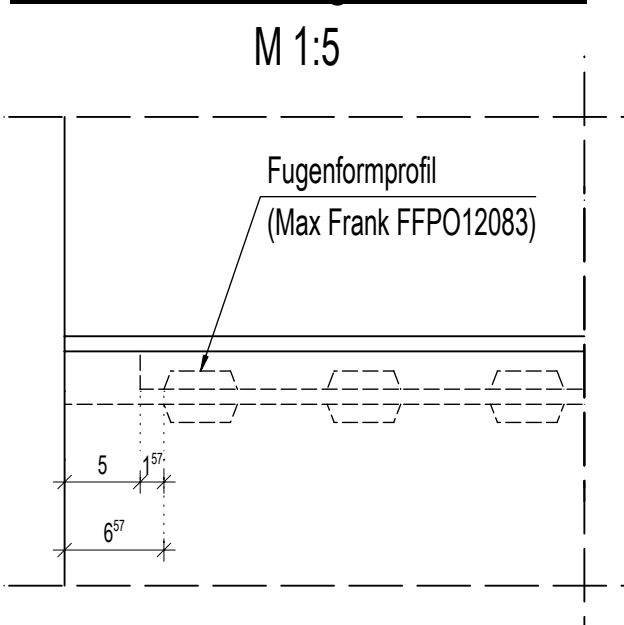


Ansicht Stoßfuge - Detail 2
M 1:5

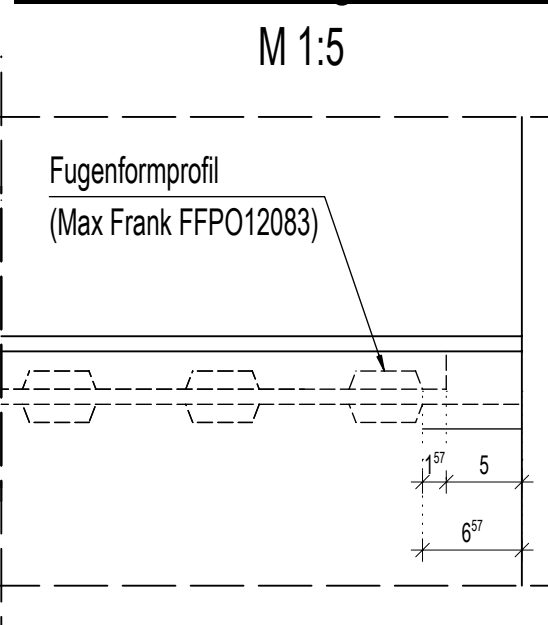


Draufsicht 1-1
M 1:25

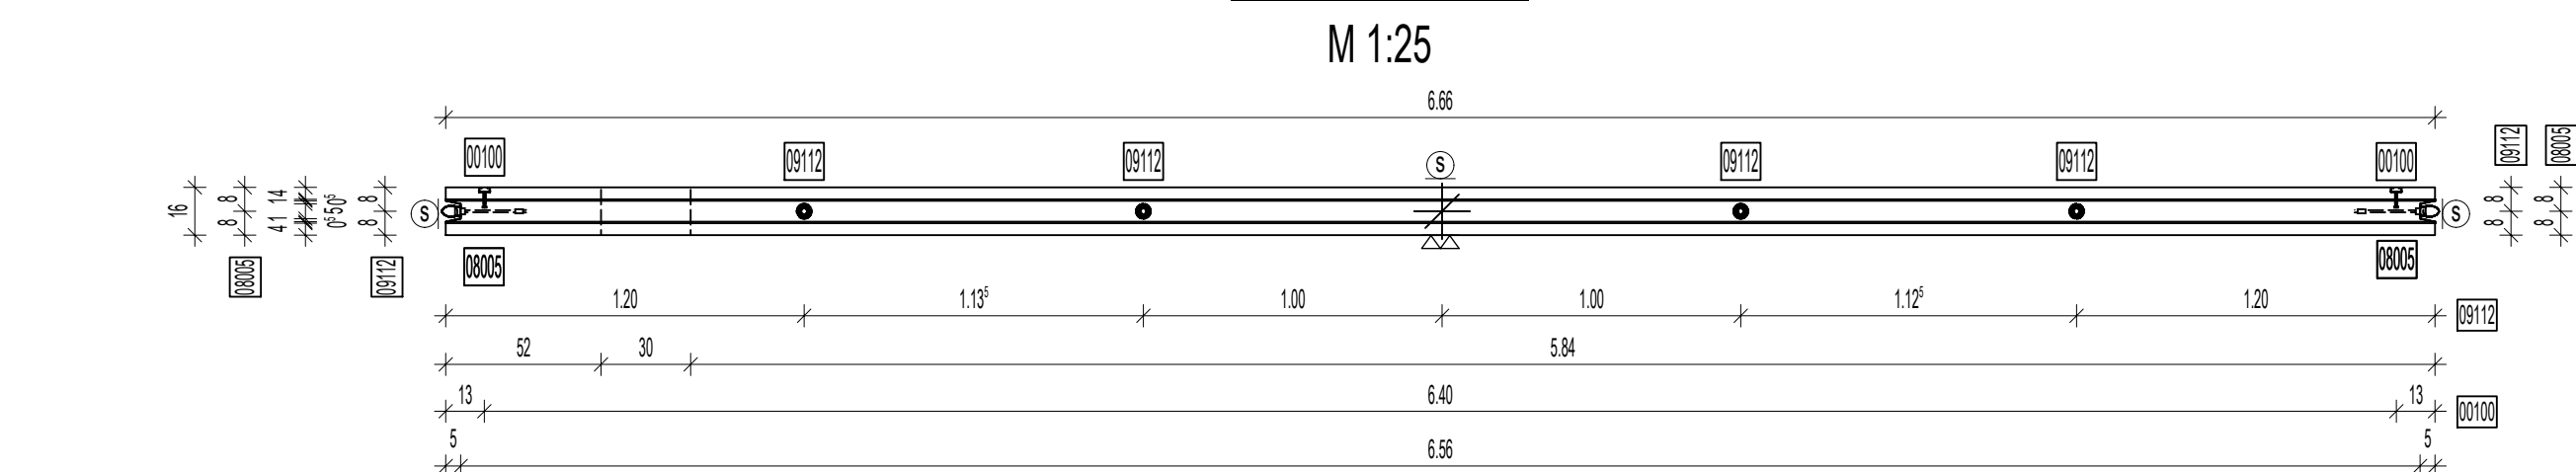


Bewehrung
M 1:25

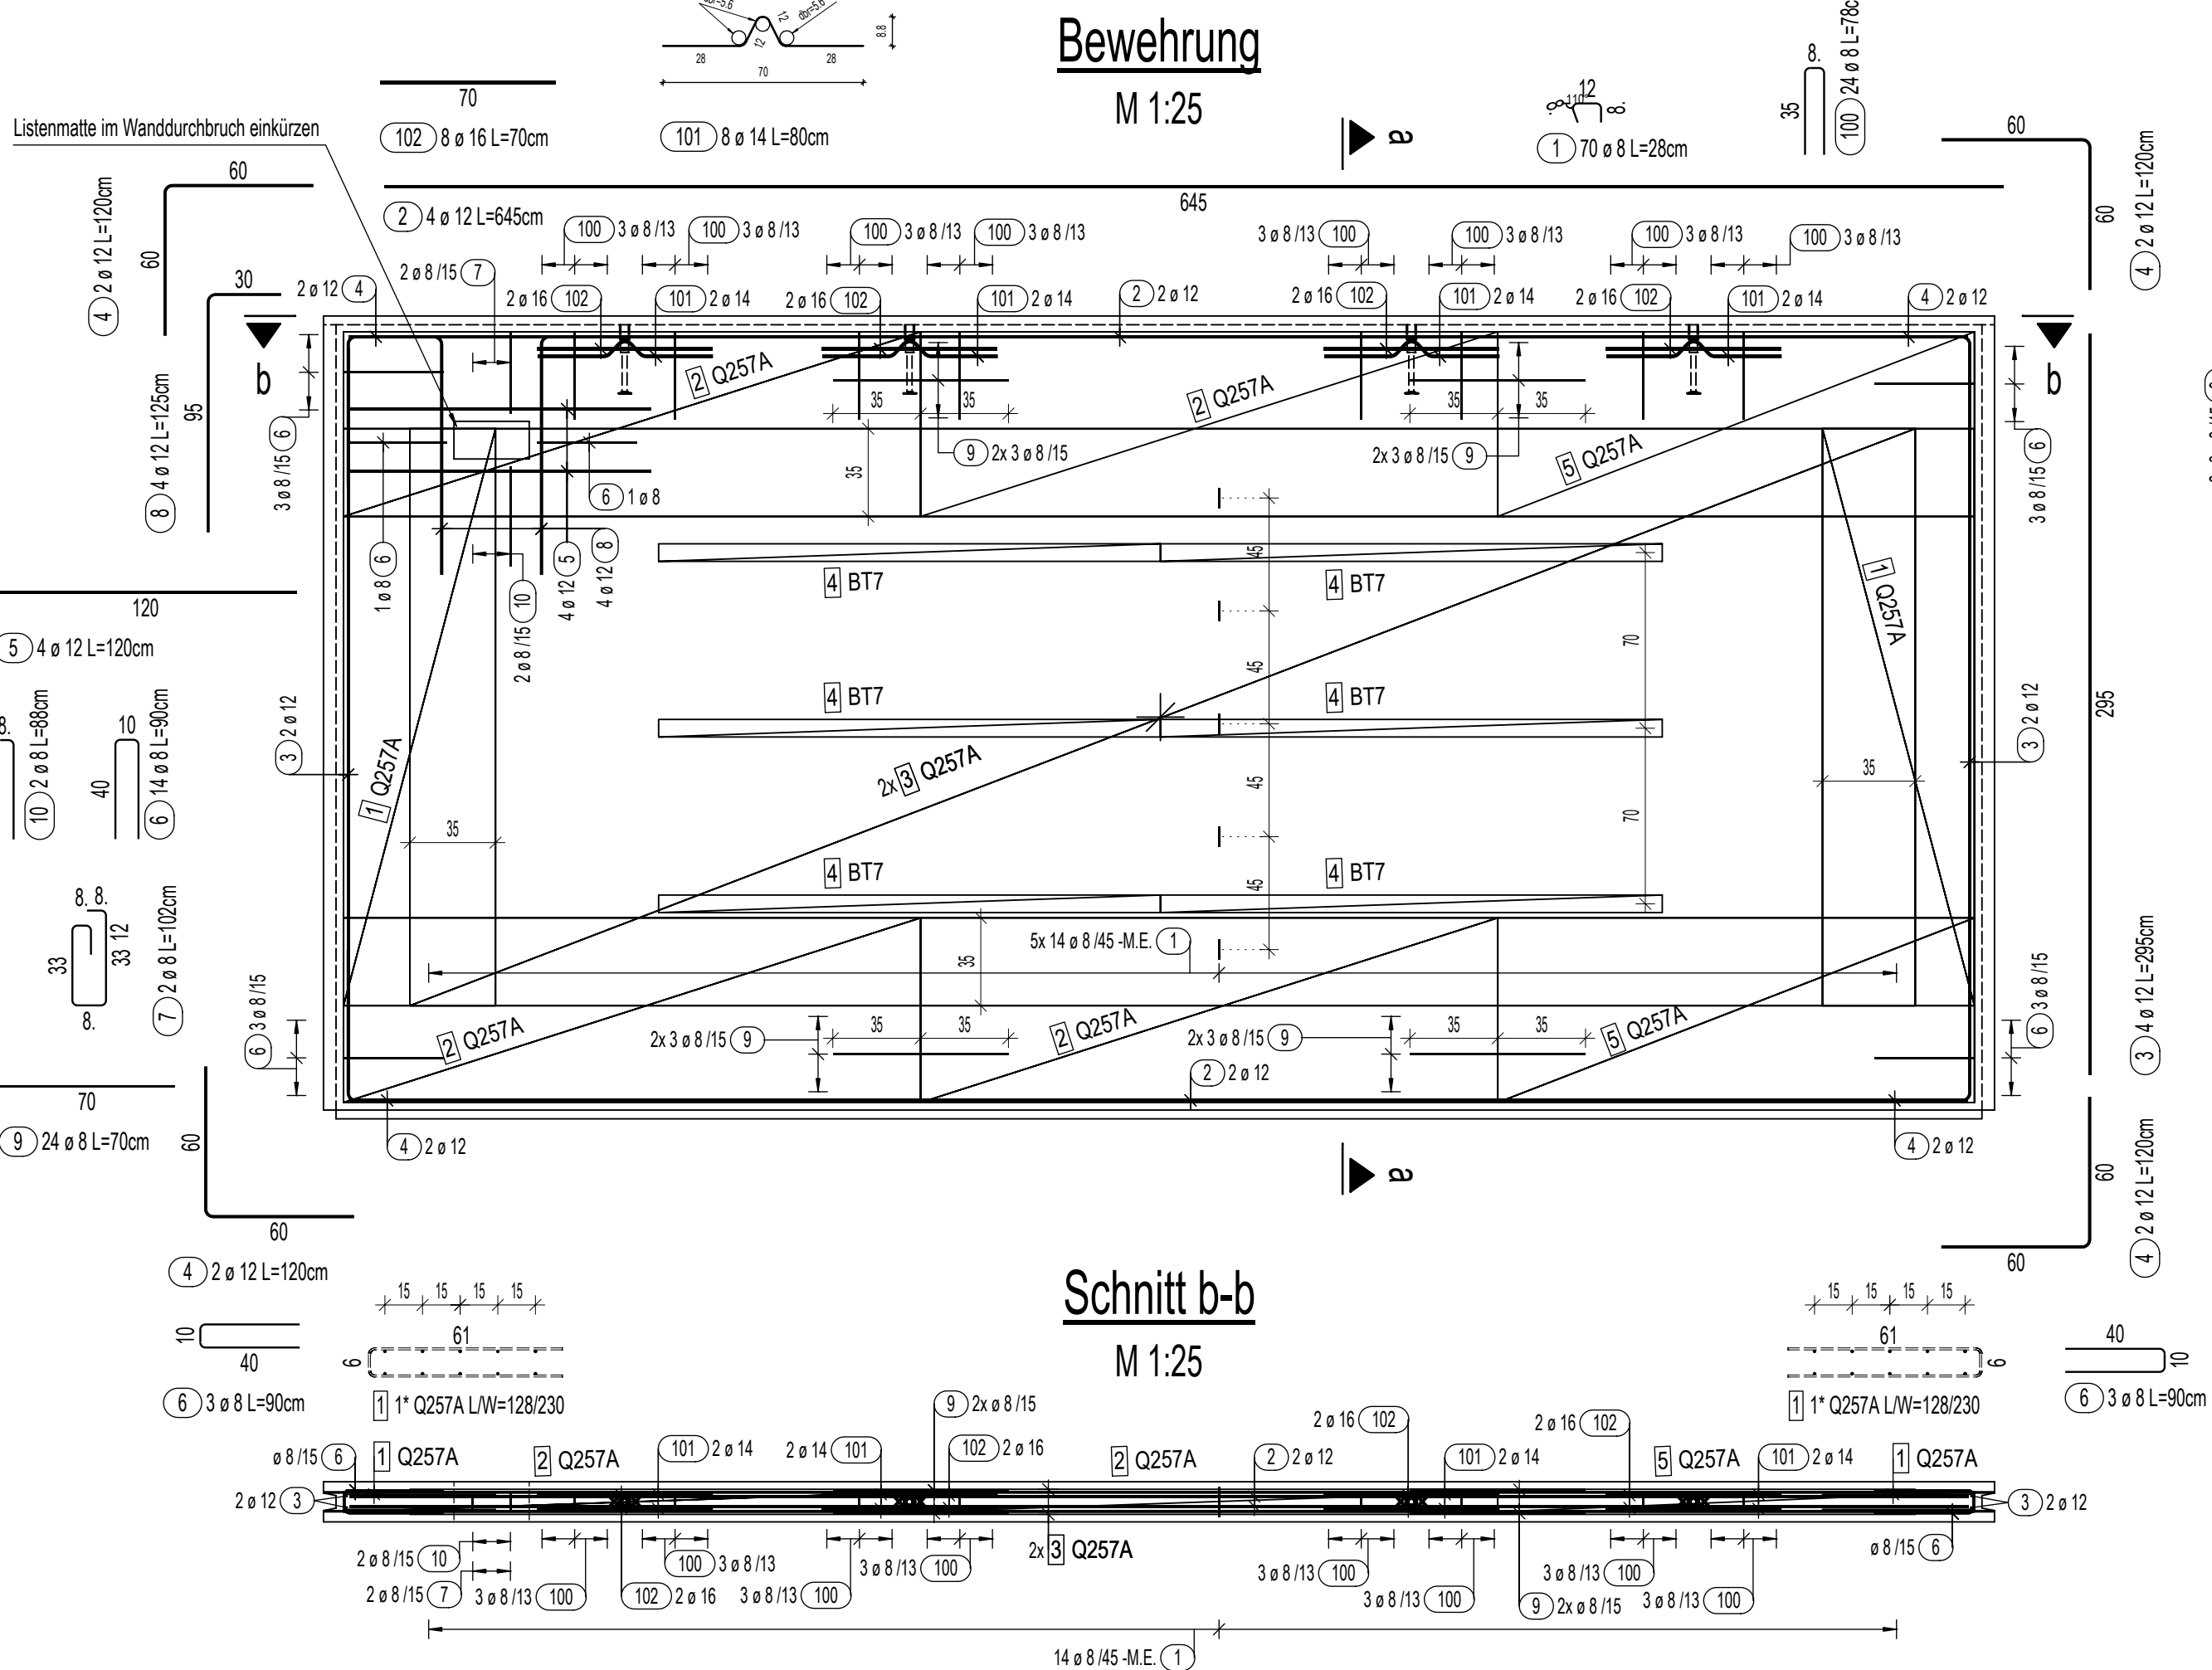

Schnitt a-a
M 1:25

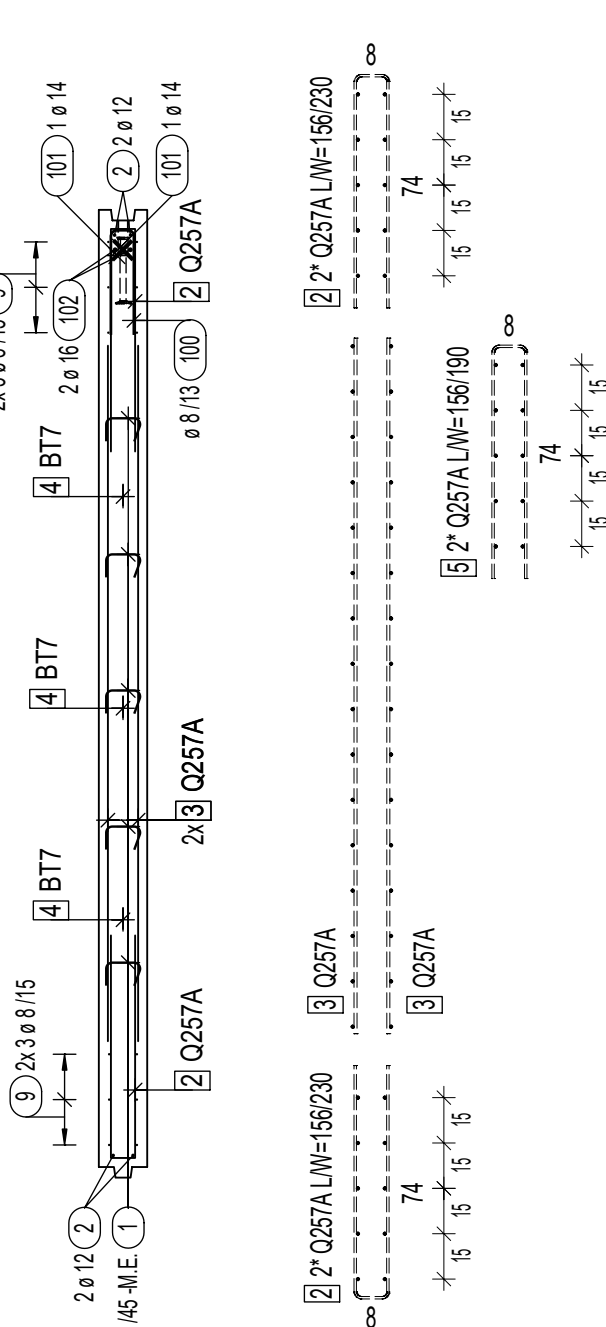

3D Perspektive
M 1:25

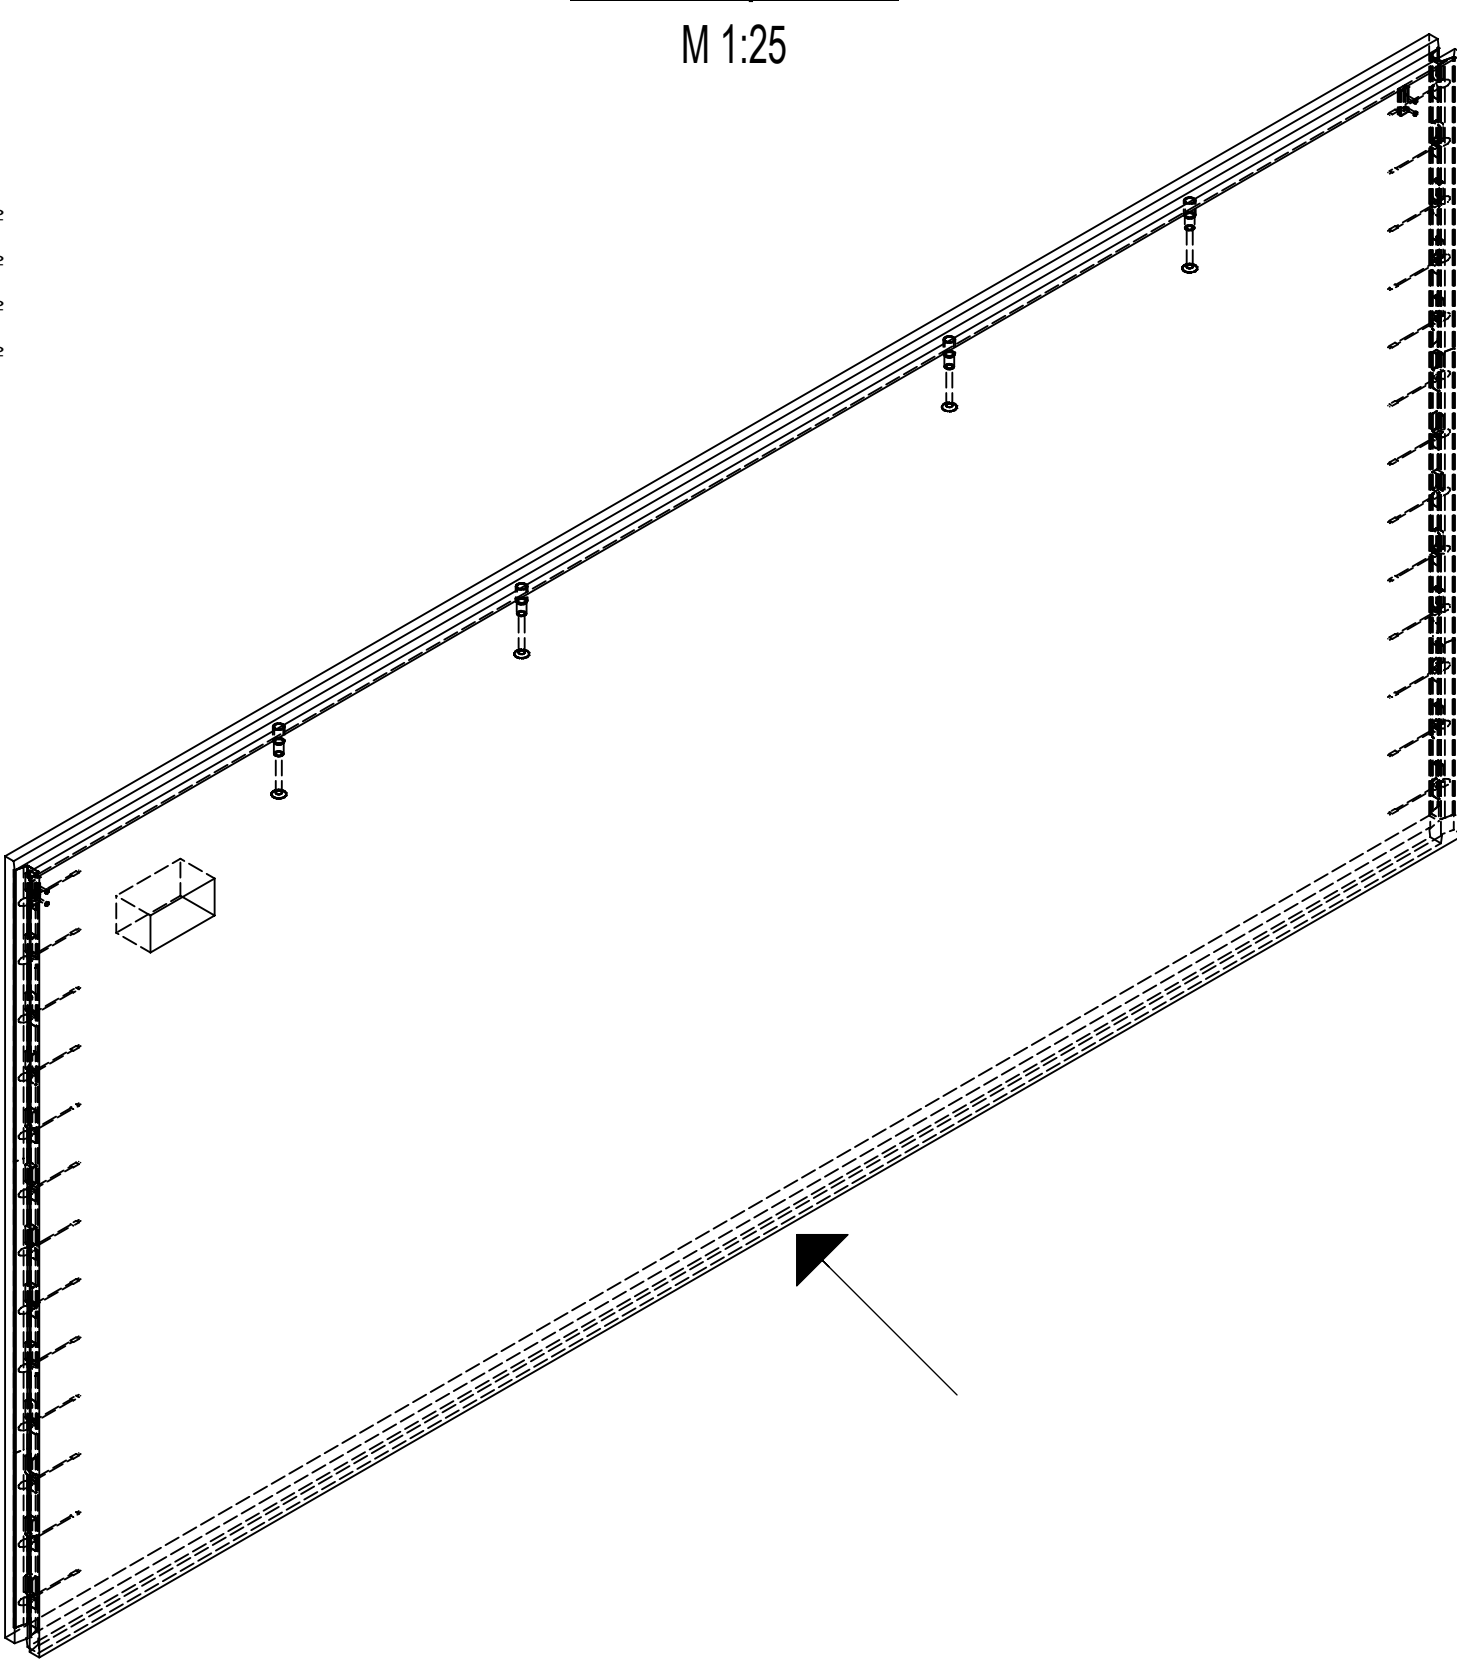

ALLGEMEINE BEMERKUNGEN:
Alle Maße sind im Plan und am Bau zu überprüfen! Abweichende oder falsche Maße sind dem Planverfasser und/oder dem Bauleiter schriftlich zu melden!
Anmerkungen gelten nur bei schriftlicher Bestätigung des Planverfassers und der Objektüberwachung als anerkannt.
Für diese Zeichnung behält sich der Planverfasser alle Rechte vor. Vervielfältigungen dürfen nur mit ausdrücklicher Genehmigung des Planverfassers erfolgen.

ABKÜRZUNGEN UND SYMBOLE


= Änderung
= in Klärung

BAUSTOFFE (SOWEIT NICHT ANDERS ANGEGEBEN)

Kanten soweit nichts anderes angegeben ist, sind zu fassen
Faserstärke: $\geq 1.5 \text{ cm}$

Strukturmaterie
Sichtbeton (SB II)
Flügelgeglättet
abgerieben
geglättet
rauh
Fugenformprofil (Max Frank FFPO12083)
schalungsglätt

MINDESTWERTE DER BIEGERADIEN DBR (EC2, TABELLE 8.1 + 8.2)

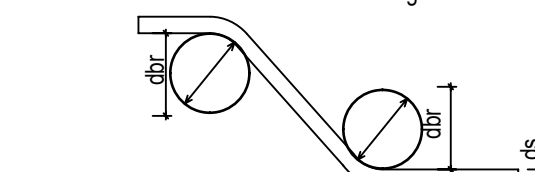Haken, Winkelhaken, Schlaufen		Stabkrümmungen	
			
Stabdurchmesser	Haken, Schlaufen, Bügel	Betondeckung rechtwinklig zur Krümmungsebene	Aufbiegungen und andere Krümmungen von Stäben (Rahmenecken)
$ds > 20\text{mm}$	7 ds	$> 100\text{ mm}$ oder $> 7ds$	10 ds
$ds \leq 20\text{mm}$	4 ds	$> 50\text{ mm}$ und $> 3ds$	15 ds
		$\leq 50\text{ mm}$ oder $\leq 3\text{ ds}$	20 ds

Die Gesamtlängen der Auszüge beziehen sich auf Außenmaße!

Die Gesamtlängen der Auszüge beziehen sich auf Außenmaße!

letzte Stabstahlposition 10 letzte Mattenposition 5

Bauteil:	Betonfestigkeit	Expositionsklassen:	Feuchtigkeitsklasse:	Betondeckung:		
				$C_{min, air}$	ΔC_{dev}	C_v
FT-Brandwand	C30/37	XC2	WO	20	10	30

Volumen	Gewicht	Anzahl	Statische Positionsnummer
3.342 m ³	8.178 T	1	HL-7-10

ZUGEHÖRIGE PLÄNE

Übersichtsplan Wandansichten
Ansichten - Brandwände Teil 6 - Achse E/9-16

REN-HL-KO-TK-W-UB-E00-4500
REN-HL-KO-TK-W-UB-E00-4506

PLAN STATUS

ZUR AUSFÜHRUNG FREIGEgeben

INDEX	DATUM	ÄNDERUNG	GEÄNDERT
01	12/09/2023	Freigabe durch Prüfingenieur am 05.09.2023 und Architekt am 30.06.2023	D.N.
00	01/06/2023	Erstauslieferung	H.D.

OKRD= ±36,50 m ü NN Bemessungsgrundwasserstand -2,20 m GOK OKFFB= ±36,50 m ü NN

Plannummer Tragwerksplanung: Projekt -Gebäude -Fachbereich -Geweik -Phase -Planart -Ebene -Plannummer -Index -Status	REN-HL-KO-TK-W-FT-E01-1577-01-F
Basisplan: Projekt:	Produktionswerk Renggli DE
Bauherr:	Renggli Deutschland GmbH Am Bahnhof Westend 9-11 14059 Berlin
Technisches Büro Heidelberger Betonelemente GmbH & Co. KG Am Zeisig 9 09322 Penig / OT Wernsdorf Tel.: 037381/857-0 Fax: 037381/857-30	HEIDELBERGER BETONELEMENTE HEIDELBERG CEMENT Group
Fachplaner:	gbc engineers GmbH Am Spreebord 9d 10589 Berlin Tel.: +49 (0) 30 339 38 740 Fax: +49 (0) 30 339 38 741 eMail: info@gbc-engineers.de
Zeichnung:	Fertigteilplan Brandwand W-577-01
Projekt-Nr.: 30-0-033	Planungsphase: Ausführungsplanung
Blattgröße: 594x841mm	gezeichnet: H.D. Datum: 01/06/2023
Maßstab: 1:5 1:25	geprüft: D.M. Datum: 01/06/2023